

Заказчик - АО «Невский экологический оператор»
Комплекс по переработке отходов «Новоселки»
**Производственный корпус.
 Цех сортировки ТКО**
РАБОЧАЯ ДОКУМЕНТАЦИЯ
**Конструкции железобетонные.
 Фундаменты под оборудование**
КПЭИ.1070/2.2-1.2-КЖ2

Изм.	№ док.	Подп.	Дата
1	4219-26		27.07.2026

 Заместитель генерального директора
 по направлению генерации

Главный инженер проекта



В.С. Кучанов

А.В. Рябич

Согласовано		
Взам. инв. №		
Подп. и дата		
Инв. № подл.		

ОБЩЕСТВО С ОГРАНИЧЕННОЙ ОТВЕТСТВЕННОСТЬЮ
«ТЭП ИВАНОВО»

Заказчик - АО «Невский экологический оператор»

Комплекс по переработке отходов «Новоселки»

**Производственный корпус.
Цех сортировки ТКО**

РАБОЧАЯ ДОКУМЕНТАЦИЯ

**Конструкции железобетонные.
Фундаменты под оборудование**

КПЭИ.1070/2.2-1.2-КЖ2

Главный инженер проекта




С.М. Сильверстов

Согласовано


Разрешение		Обозначение		КПЭИ.1070/2.2-1.2-КЖ2				
4219-26		Наименование объекта строительства		Комплекс по переработке отходов «Новоселки»				
Изм.	Лист	Содержание изменения			Код	Примечание		
1		<u>КПЭИ.1070/2.2-1.2-КЖ2</u>			1	Изменения внесены на основании письма № 718 от 21.07.2026		
	1	Внесены данные об изменении в ведомость рабочих чертежей основного комплекта						
	2	Откорректирован габарит фундамента ФМПЗ						
	6	Откорректирован габарит фундамента ФМПЗ						
	7	Откорректировано армирование фундамента ФМПЗ						
Изм. внес	Висицкая		27.07.26	ООО «ТЭП Иваново»			Лист	Листов
Составил	Висицкая		27.07.26					
ГИП	Сильверстов		27.07.26					
								1

Схема расположения фундаментов оборудования





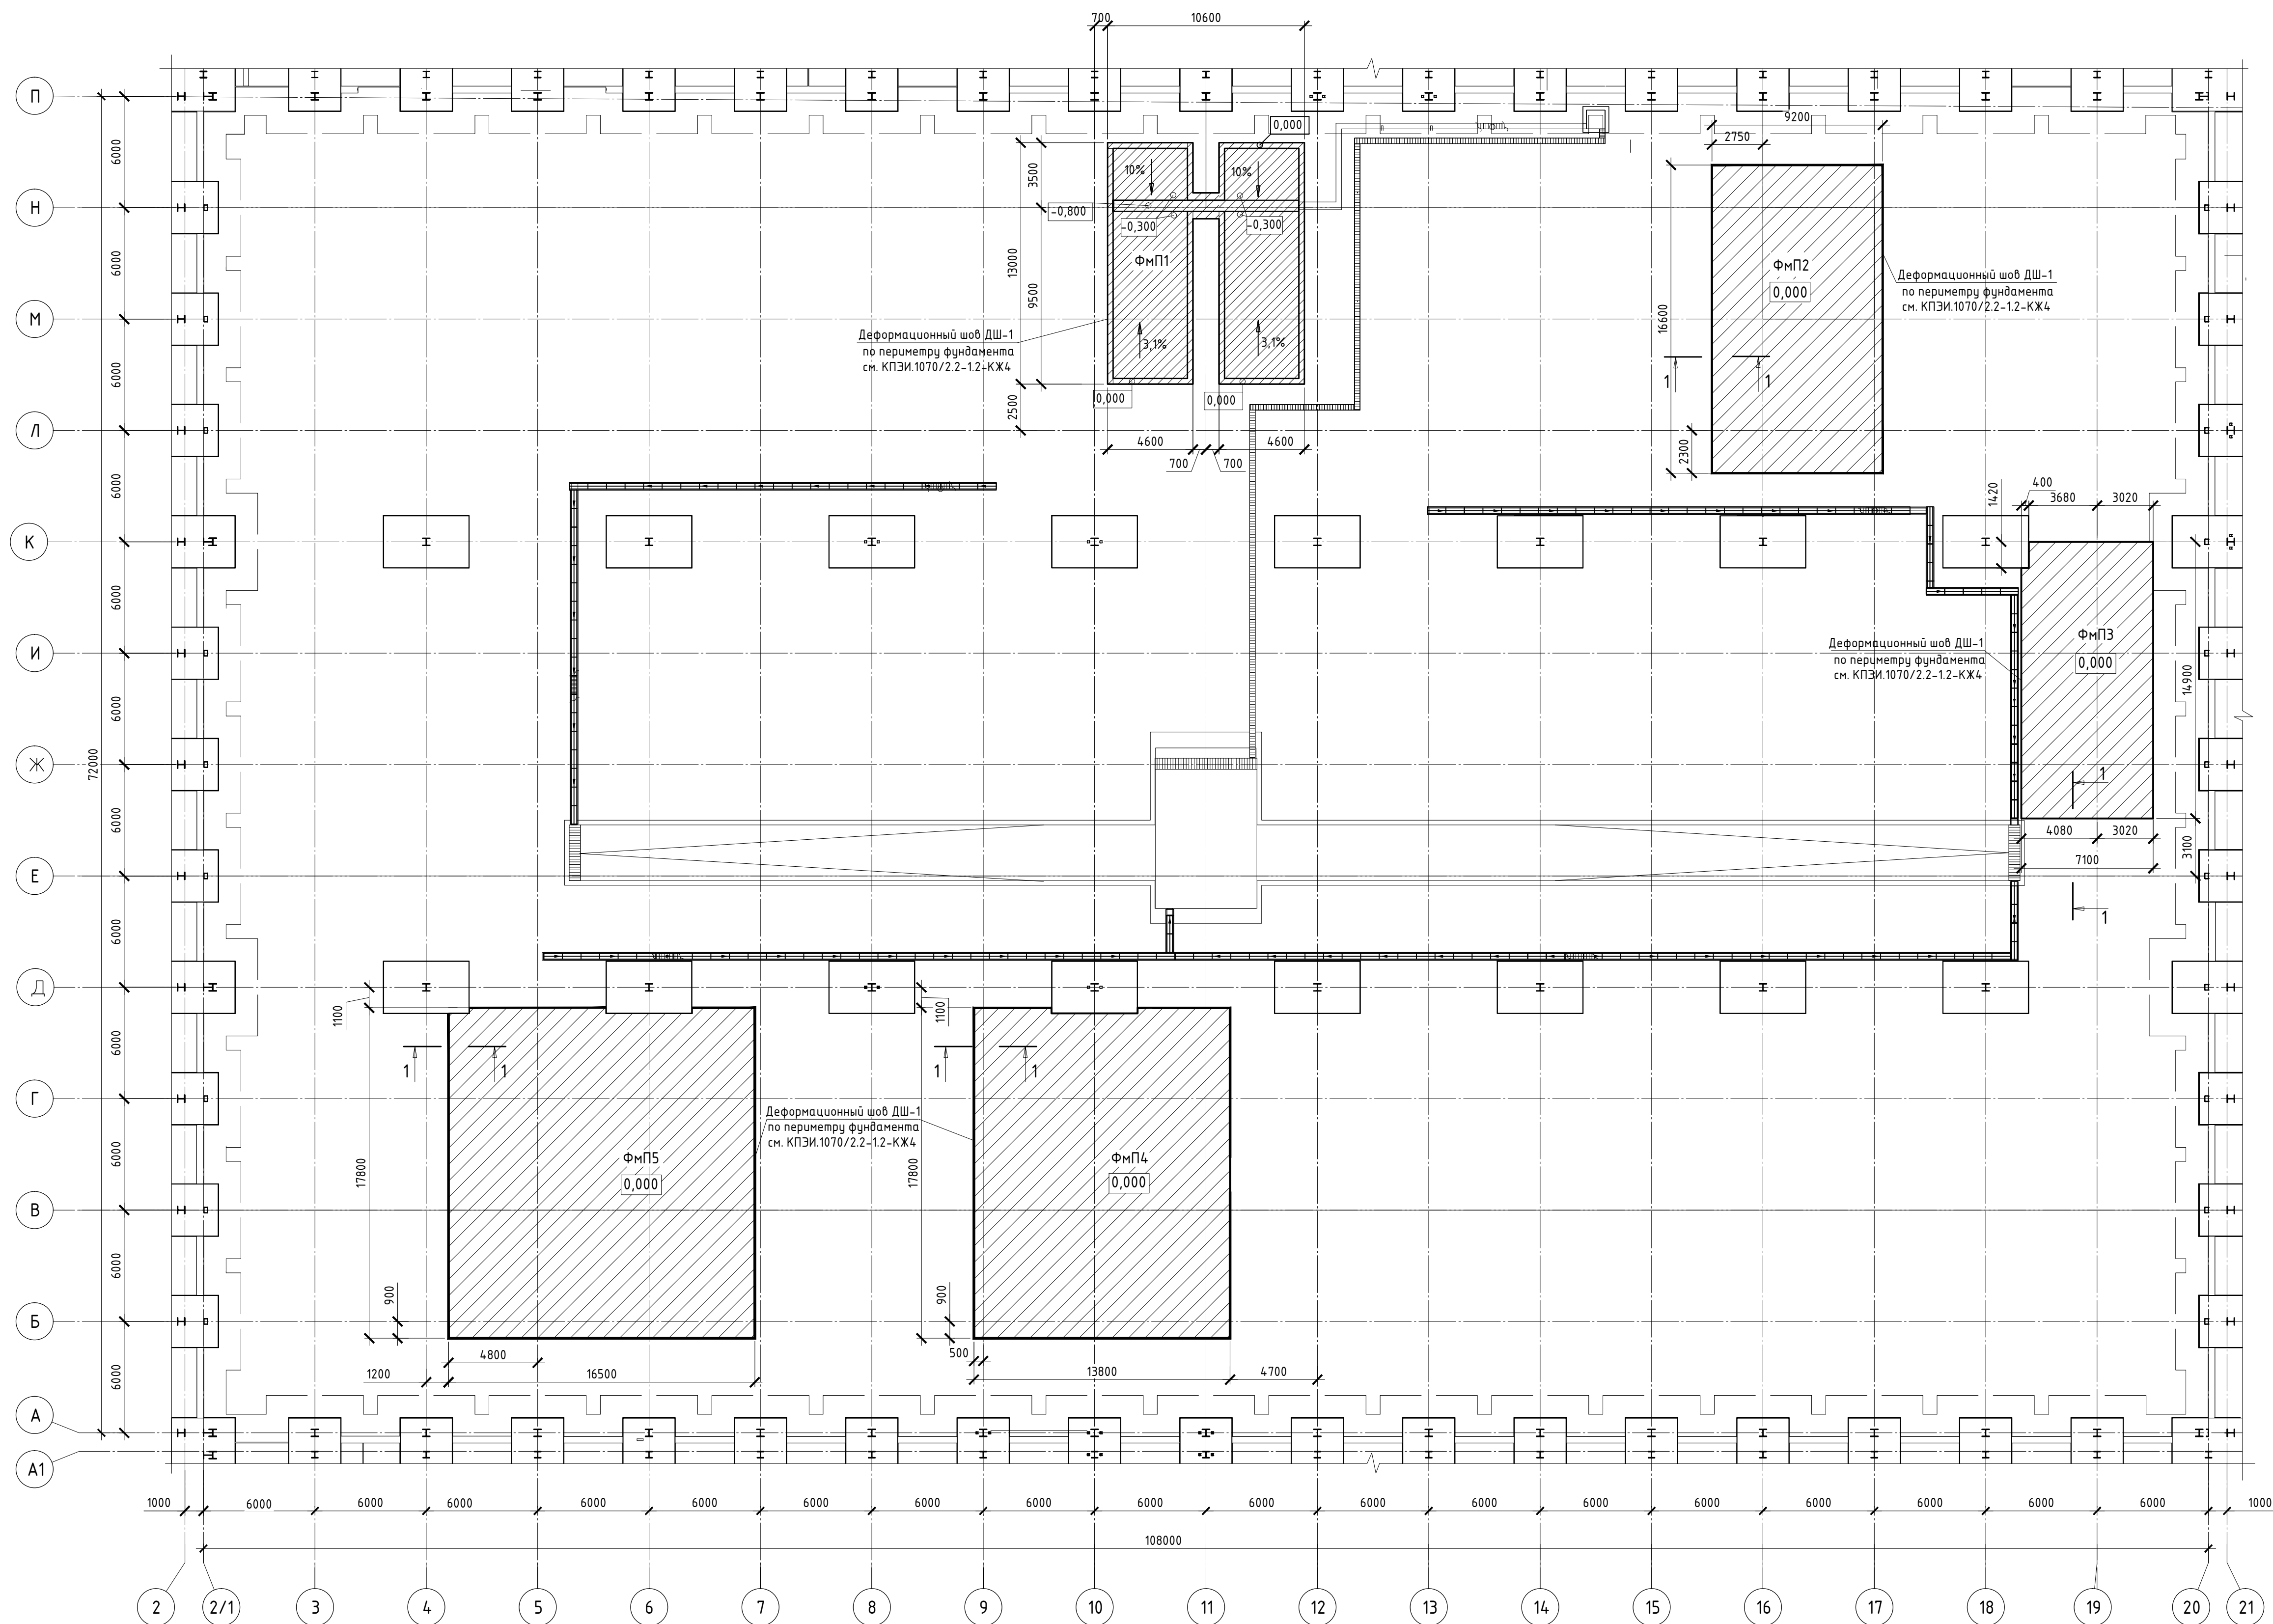


Спецификация элементов

Поз.	Обозначение	Наименование	Кол.	Масса ед. кг	Прим.
Фмп1	КПЭИ.1070/2.2-1.2-КЖ2 лист 3	Фундамент Фмп1	1		
Фмп2	КПЭИ.1070/2.2-1.2-КЖ2 лист 4	Фундамент Фмп2	1		
Фмп3	КПЭИ.1070/2.2-1.2-КЖ2 лист 6	Фундамент Фмп3	1		
Фмп4	КПЭИ.1070/2.2-1.2-КЖ2 лист 8	Фундамент Фмп4	1		
Фмп5	КПЭИ.1070/2.2-1.2-КЖ2 лист 10	Фундамент Фмп5	1		

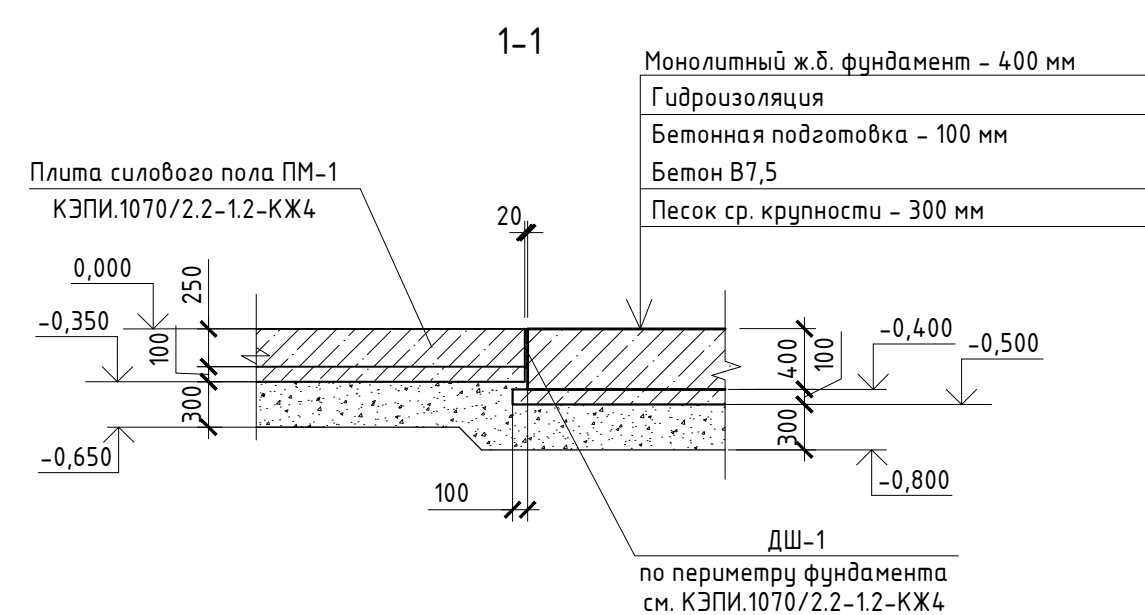

						КПЭИ.1070/2.2-1.2-КЖ2			
1	-	Зам. 4.219-26	<i>SP</i>	27.07.24	Комплекс по переработке «Новоселки»				
Изм.	Кол-во	Лист	№ док.	Подпись	Дата				
Разраб.	Вислицкий	<i>SP</i>		04.26	Производственный корпус. Цех сортировки ТК0	Стандия	Лист	Листов	
Проверил	Вислицкий	<i>См</i>		04.26		Р	2		
Н. контр.	Вислицкий			04.26	Схема расположения фундаментов оборудования	ООО «ТЭП ИВАНОВО»			
ГИП	Сильверстов	<i>Сильверстов</i>		04.26					

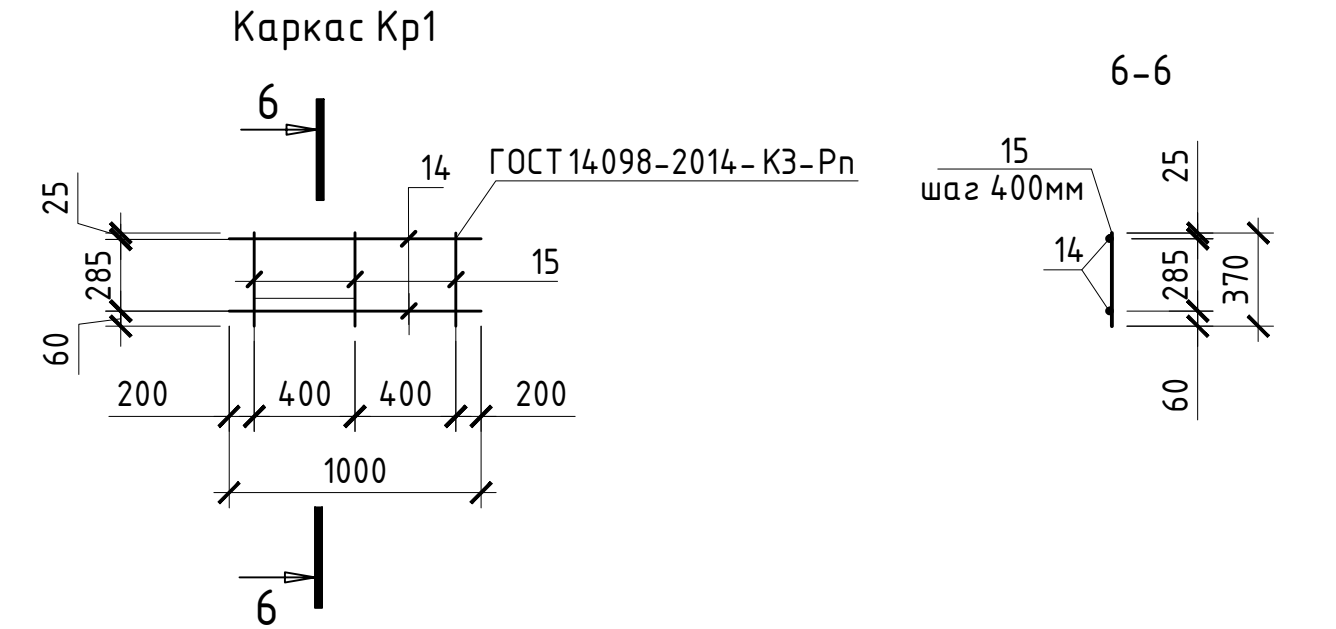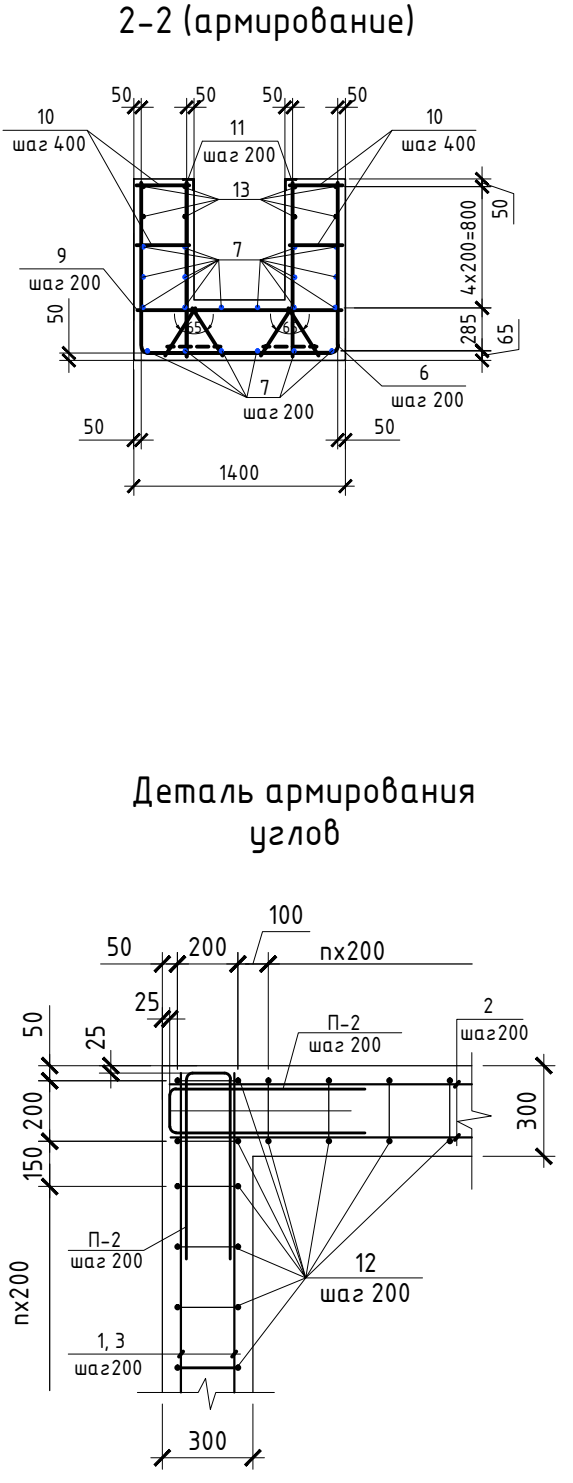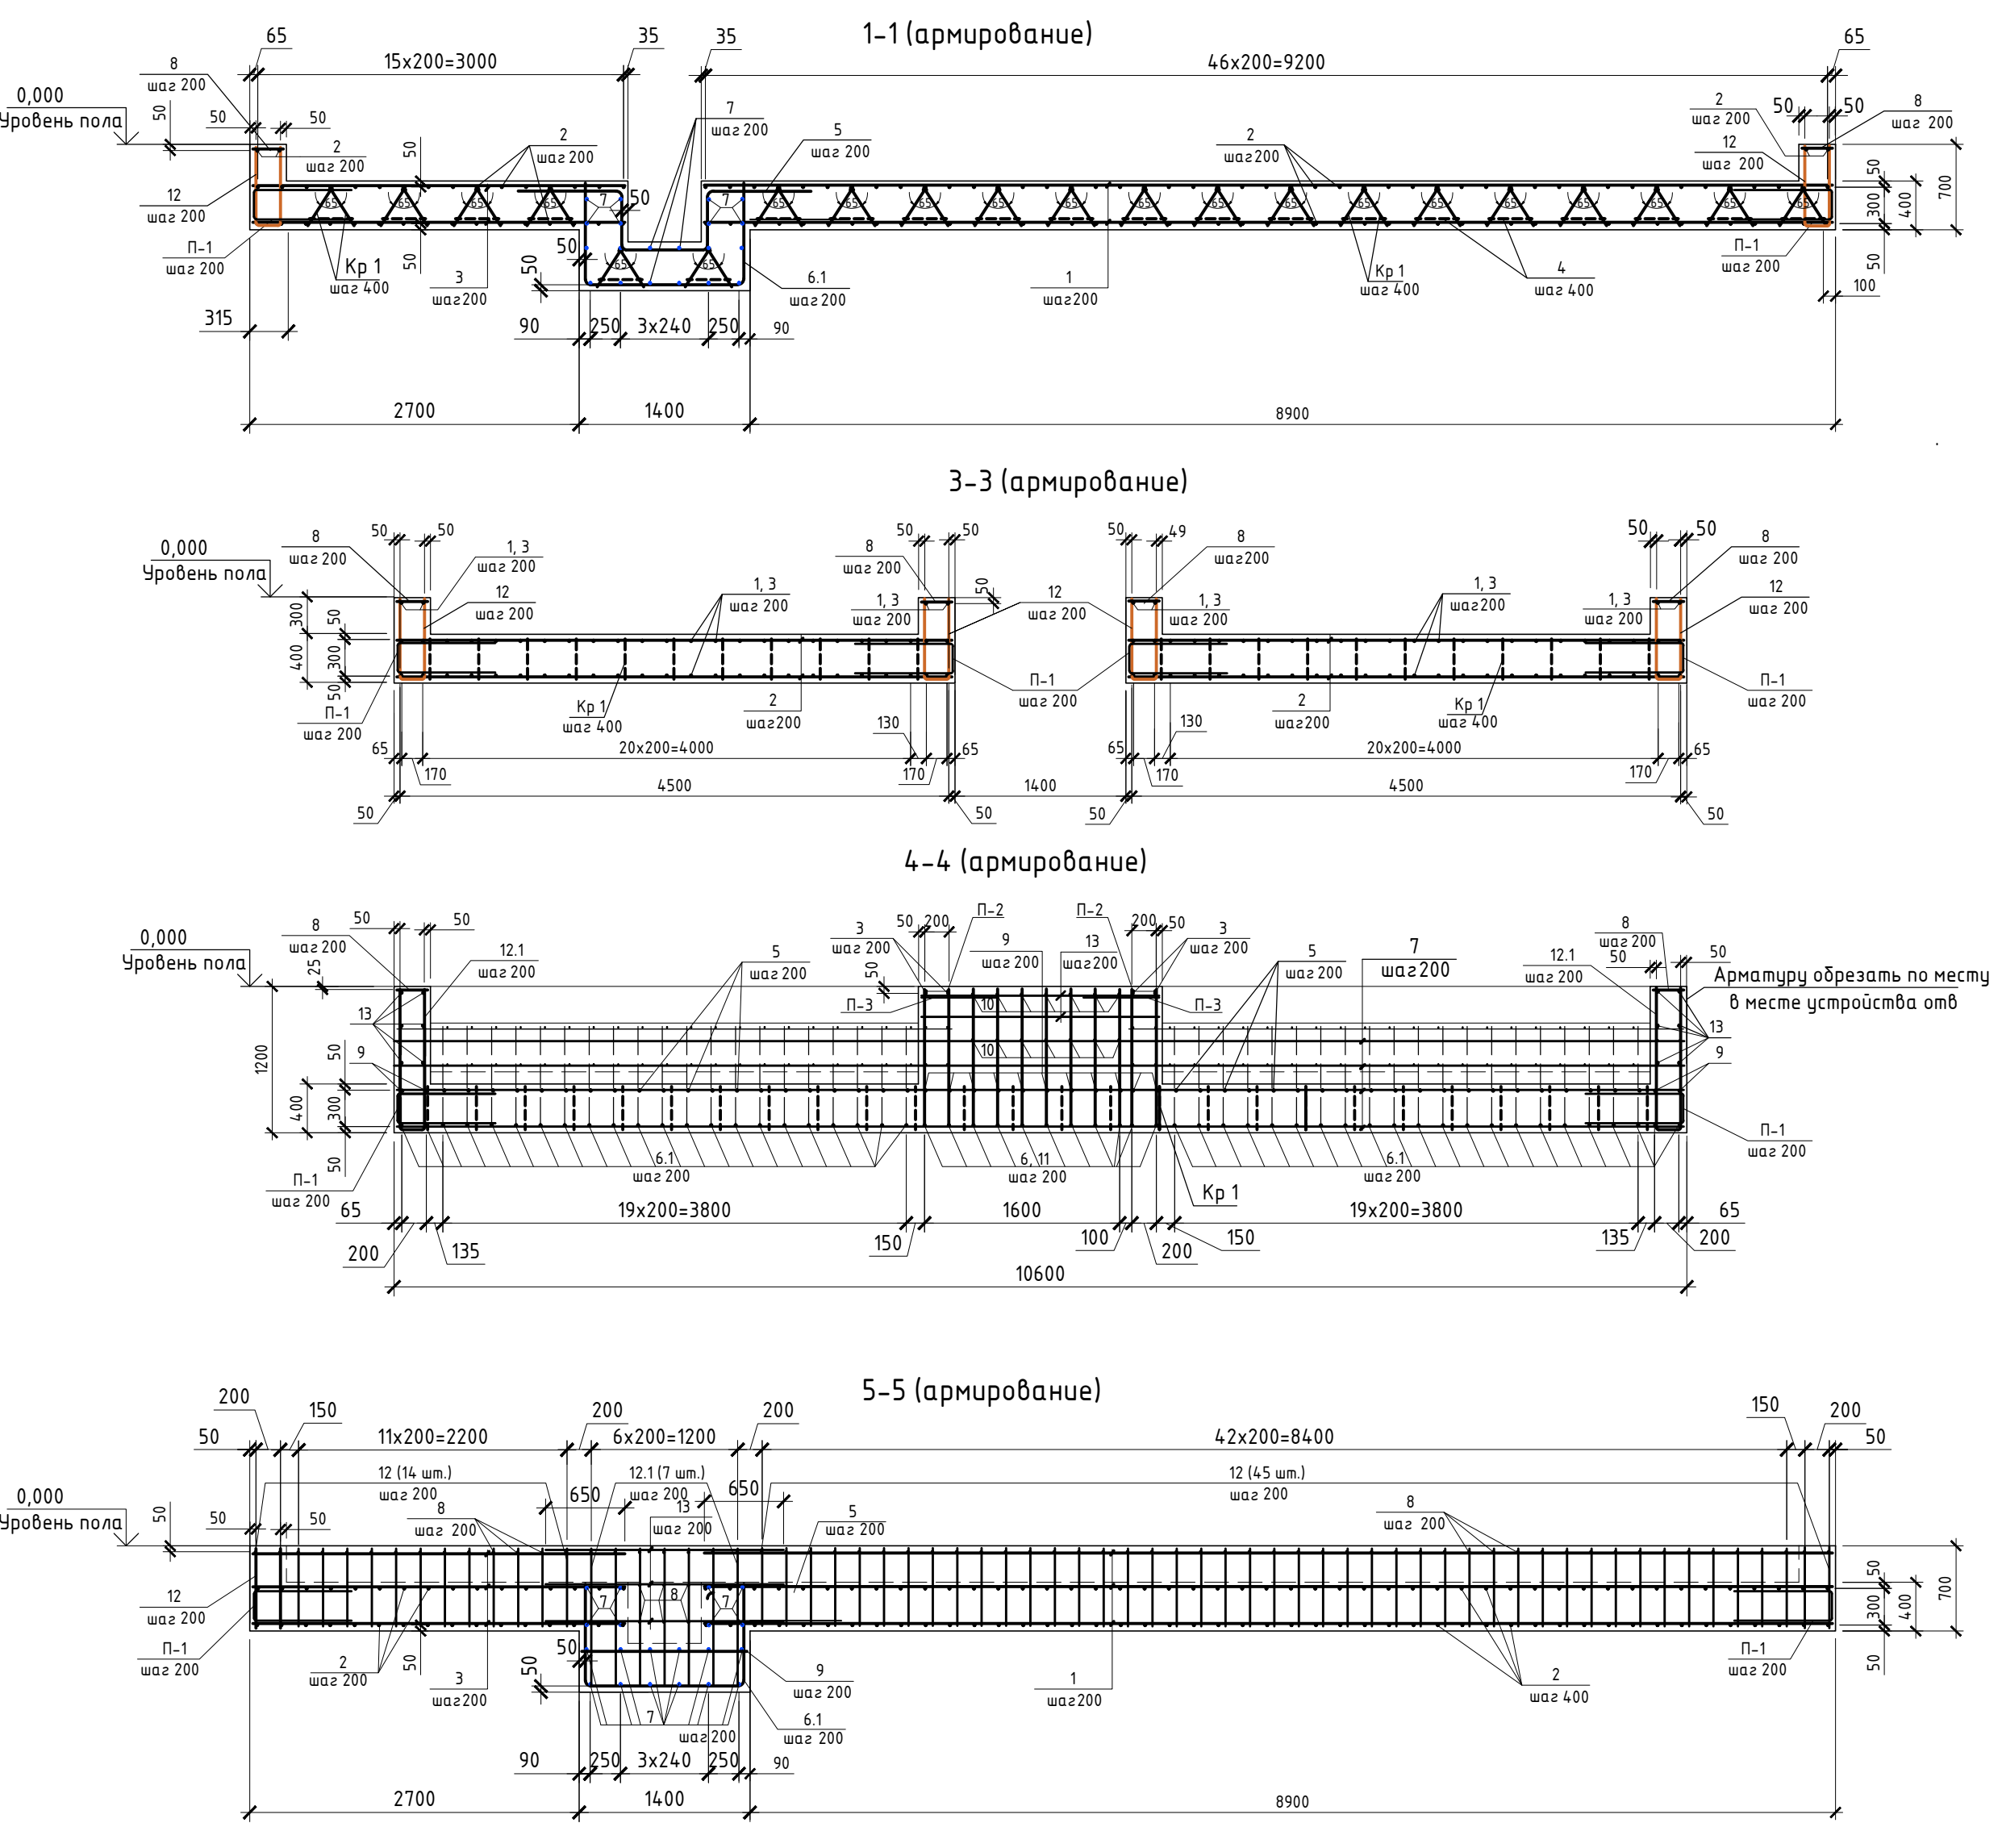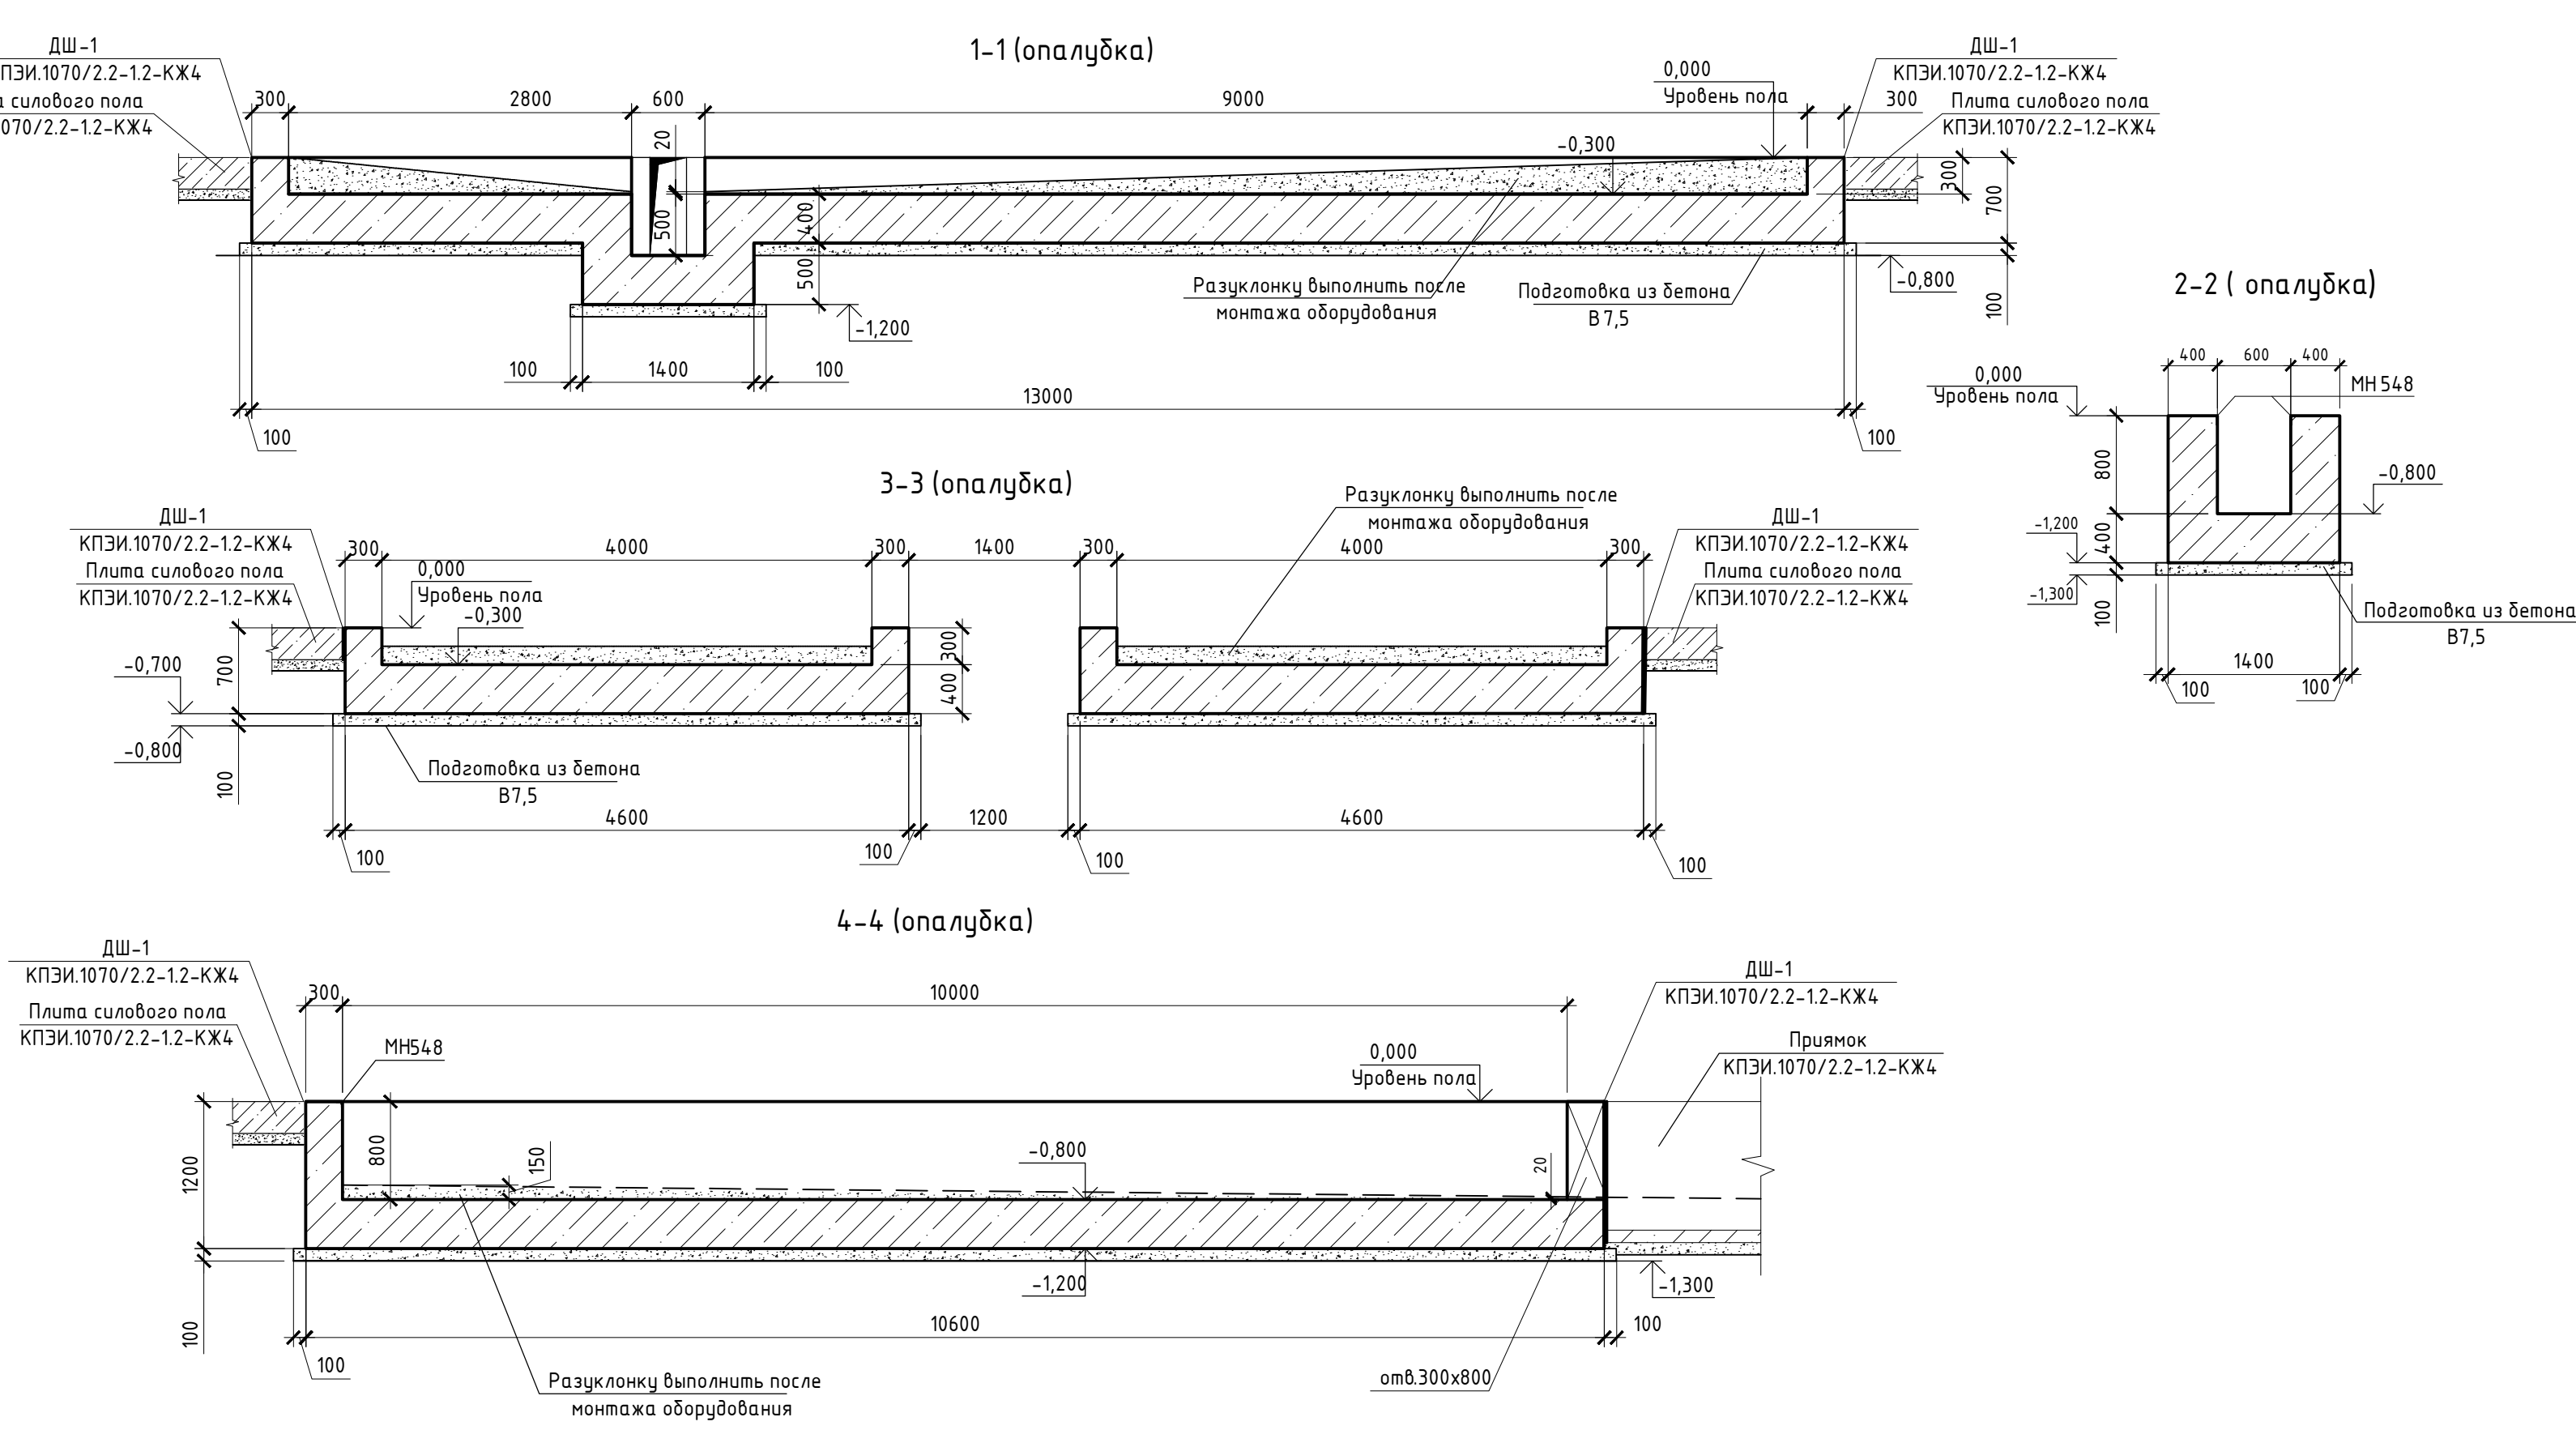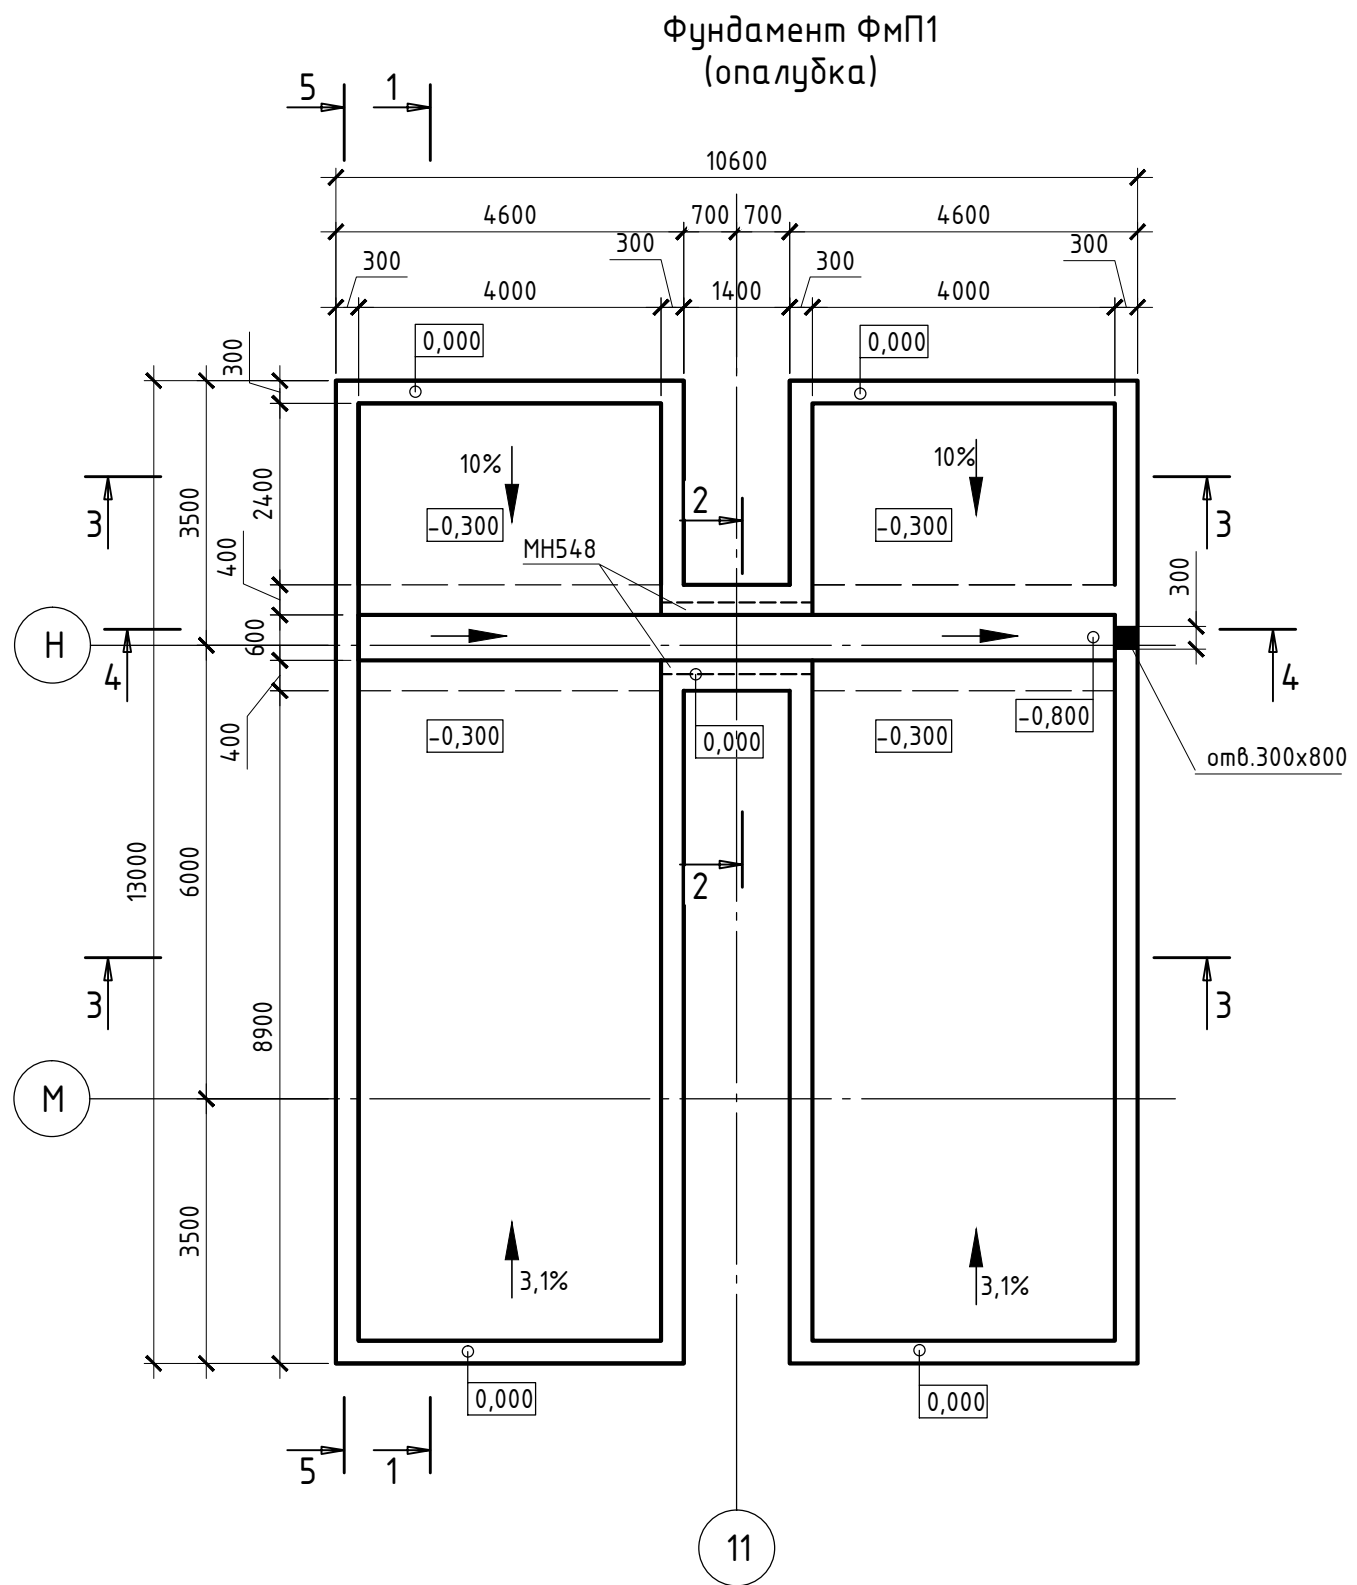

Ведомость деталей		Ведомость деталей	
Поз.	Эскиз	Поз.	Эскиз
5		12	
6		12.1	
6.1		П-2	
П-1		П-3	

Спецификация элементов монолитного фундамента ФМП1						
Поз.	Обозначение	Наименование	Кол.	Масса ед. кг	Прим.	
Кр1		Каркас Кр1	206,0	2,3	м.п.	
МН548	Серия 1.400-15 вып.1	Закладная деталь	4,00	4,2	м.п.	
1	ГОСТ 34028-2016	12-A500C	l=9250	104	8,24	
2	ГОСТ 34028-2016	12-A500C	l=4550	130	4,232	
3	ГОСТ 34028-2016	12-A500C	l=3050	104	2,71	
4	ГОСТ 34028-2016	12-A500C	l=350	451	0,31	
5	ГОСТ 34028-2016	12-A500C	l=2952	40	2,98	
6	ГОСТ 34028-2016	12-A500C	l=3574	11	3,18	
6.1	ГОСТ 34028-2016	12-A500C	l=2974	44	2,64	
7	ГОСТ 34028-2016	12-A500C	l=10550	20	9,39	
8	ГОСТ 34028-2016	12-A500C	l=250	342	0,22	
9	ГОСТ 34028-2016	12-A500C	l=1350	15	1,20	
10	ГОСТ 34028-2016	12-A500C	l=350	28	0,31	
11	ГОСТ 34028-2016	12-A500C	l=1150	22	1,02	
12	ГОСТ 34028-2016	12-A500C	l=1524	316	1,36	
12.1	ГОСТ 34028-2016	12-A500C	l=2524	14	2,25	
13	ГОСТ 34028-2016	12-A500C	l=1950	20	1,75	
П-1	ГОСТ 34028-2016	12-A500C	l=1912	34,4	0,71	
П-2	ГОСТ 34028-2016	12-A500C	l=1408	20	1,26	
П-3	ГОСТ 34028-2016	12-A500C	l=1522	4	1,36	
Материалы:						
	ГОСТ 26633-2015	Бетон В25 П4 F150 W8	м³	56,0		
	ГОСТ 26633-2015	Бетон В7,5	м³	13,0		
	ГОСТ 8736-2025	Песок ср.крупности	м³	44,0		
	ТУ 5775-011-17925162-2003	Праймер битумный ТЕХНОНИКОЛЬ №01	52,8 м²	15,9	0,3 л/м²	
	ТУ 5775-034-17925162-2005	Битумная мастика ТЕХНОНИКОЛЬ №24 (2 слоя)	52,8 м²	105,6	2,0 кг/м² (на 2 слоя)	

Спецификация каркаса Кр1				
Поз.	Наименование	Кол.	Масса ед. кг	
14	10-A500C ГОСТ 34028-2016 l=1000	2	0,62	
15	12-A500C ГОСТ 34028-2016 l=370	3	0,33	



Ведомость расхода стали									
Марка элемента	Изделия арматурные			Закладные изделия				Всего	Общий расход
	Арматура класса			Прокат марки		Арматура класса			
	A500C			C 245		A500C			
	ГОСТ 34028-2016			ГОСТ 8509-93		ГОСТ 34028-2016			
	φ10	φ12	Итого	50х5	Итого	φ8	Итого		
ФмП1	255.44	8323.3	8578.74	15.08	15.08	1.72	1.72	16.80	8595.54

- Общие указания см. на листе 1.
- Данный лист см. совместно с листами 2, 5.
- Боковые поверхности фундамента обработать гидроизоляционной мастикой Технониколь №24 (МГТН) за 2 раза по слою битумного праймера Технониколь №01. Расход мастики 1,0 кг/м² (на 1 слой), праймера - 0,3 л/м².
- Сварку каркасов Кр1 производить в постройных условиях контактно-точечной электросваркой в соответствии с требованиями ГОСТ 15878-79. Для поддерживающих каркасов установить распорки (по 4), связывающих каркасы в уровне нижних продольных стержней. Крепление стержней к каркасам выполняется при помощи вязальной проволоки (расход 8,8 кг). Каркасы Кр1 монтировать на расстоянии не более 1000 мм.
- Объединение арматурных изделий и элементов фундамента в единую пространственную конструкцию выполнять вязкой ожеженной стальной проволокой d=1,2 мм (ГОСТ 3282-74*). Расход 150,5 кг.
- Класс бетонной поверхности принят А5 по ГОСТ 13015-2012.
- Разуклонку поверхности фундамента выполнь из цементно-песчаного раствора М200 (V=14,12м.куб.) после монтажа оборудования.
- Крепление оборудования к фундаментам предусмотрено анкер-шпильками. Места крепления, количество и марку анкеров см. раздел ТР 24.150.04_2026.06.24 000 "Экомаш"

КПЭИ.1070/2.2-1.2-КЖ2					
Комплекс по переработке «Новоселки»					
Изм.	Кол.чт.	Лист	№ док	Подпись	Дата
Разраб.	Висущая	04.26			
Проверил	Висущий	04.26			
Н. контр.	Висущий	04.26			
ГИП	Сильверстов	04.26			
Производственный корпус. Цех сортировки ТК0				Стадия	Лист
Фундамент ФМП1				Р	З
				ООО «ТЭПИВАНОВО»	

Согласовано	Взам. инв. №	Подп. и дата	Имя, № подл.

Согласовано		
	Взам. инв. №	
Подп. и дата		
	Инв. № подл.	

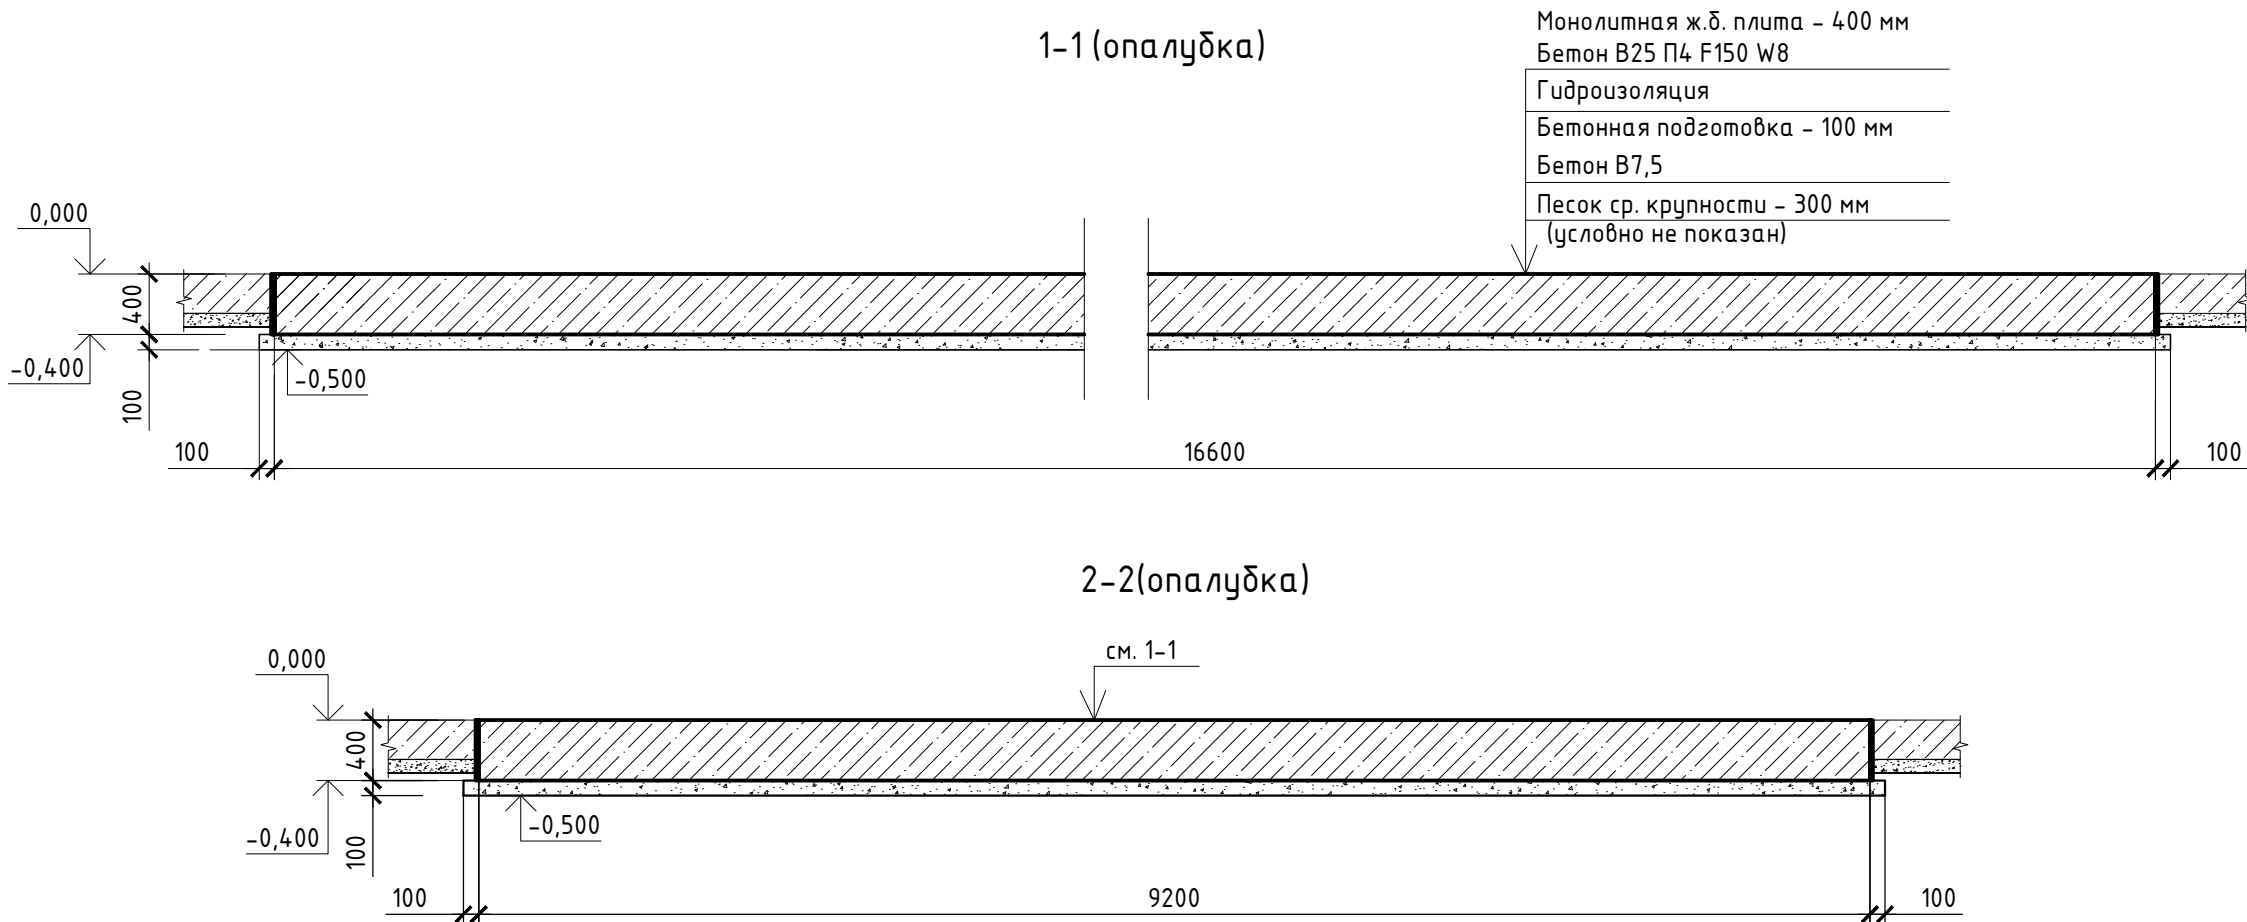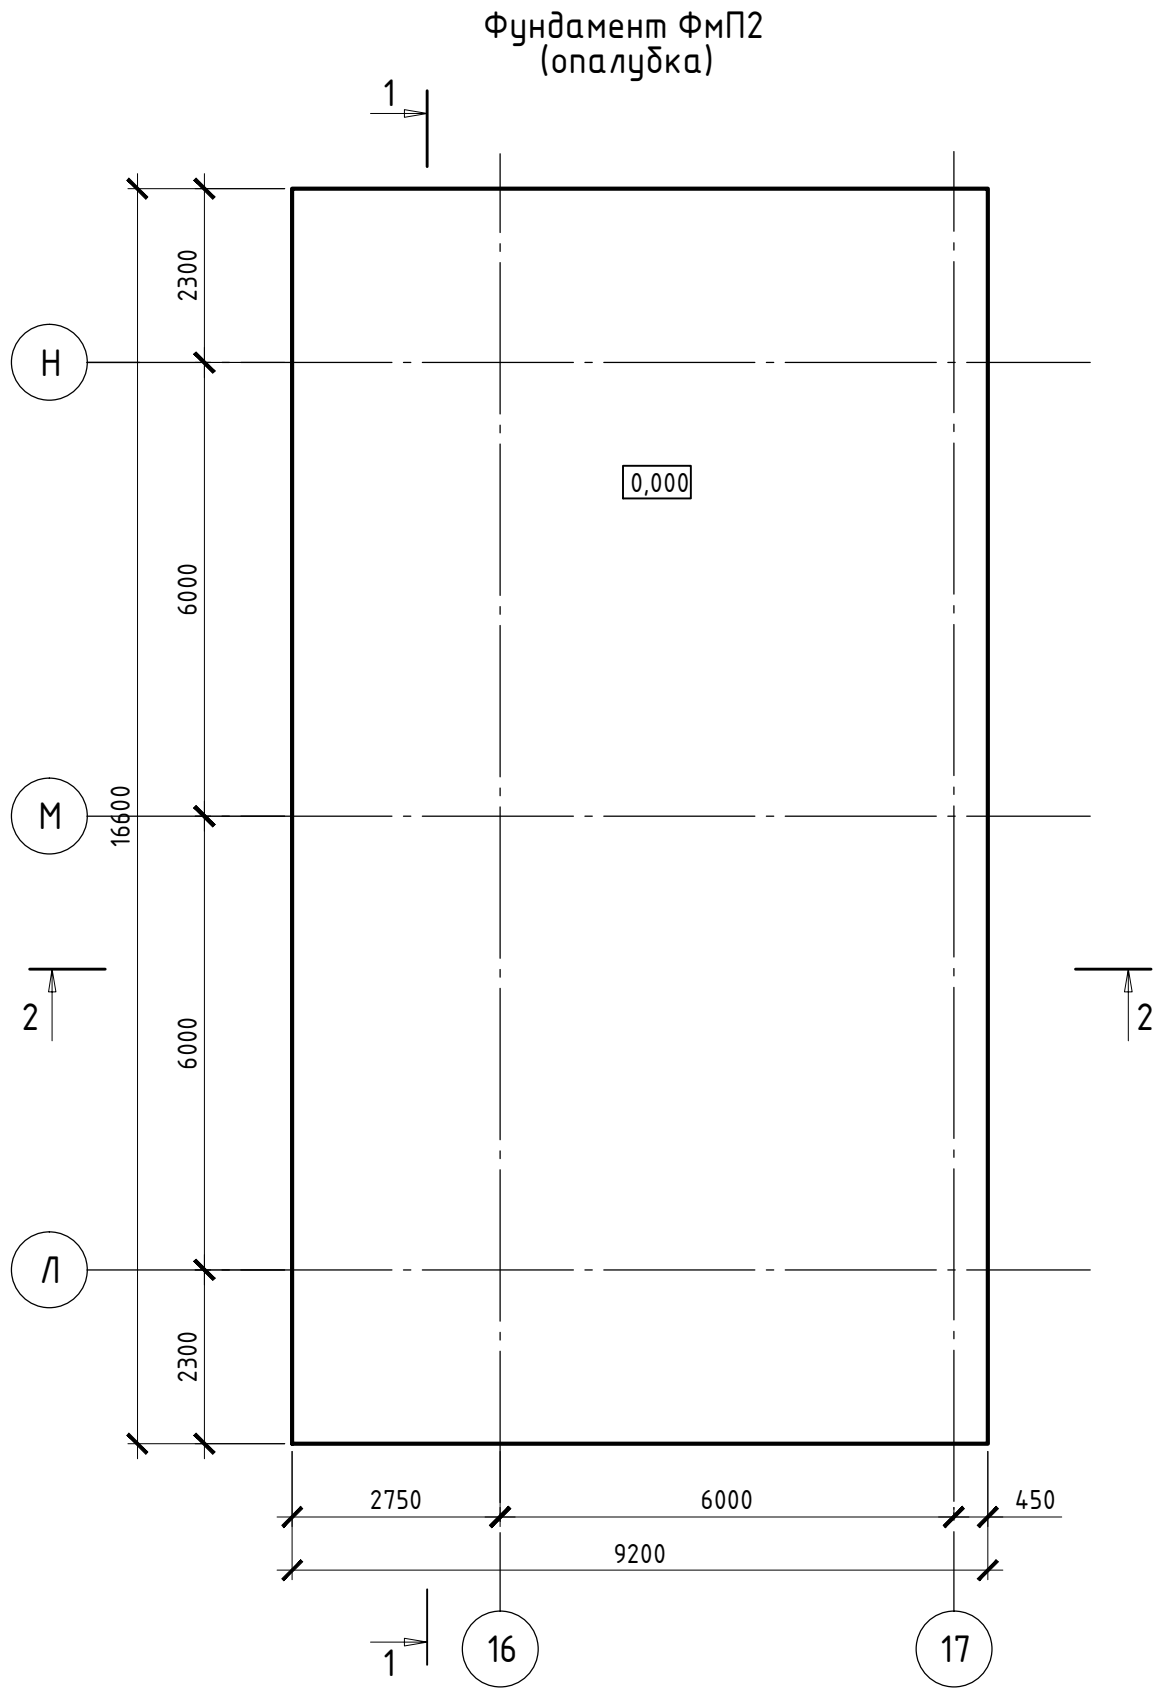

Спецификация элементов монолитного фундамента ФМП2


Поз.	Обозначение	Наименование	Кол.	Масса ед. кз	Прим.
		Материалы:			
	ГОСТ 26633–2015	Бетон В25 П4 F150 W8	м³	61,1	
	ГОСТ 26633–2015	Бетон В7,5	м³	15,8	
	ГОСТ 8736–2025	Песок ср.крупности	м³	47,4	
	ТУ 5775–011-17925162–2003	Праймер битумный ТЕХНОНИКОЛЬ №01	173,4 м²	52,1	0,3 л/м²
	ТУ 5775–034–17925162–2005	Битумная мастика ТЕХНОНИКОЛЬ№24 (2слоя)	173,4 м²	346,8	2,0 кг/м² (на 2 слоя)

- Общие указания см. на листе 1.
- Данный лист см. совместно с листами 2, 5.
- Боковые поверхности фундамента и горизонтальную поверхность бетонной подготовки обработать гидроизоляционной мастикой Технониколь №24 (2 слоя) по слою битумного праймера. Расход мастики–1,0 кг/м² (на 1 слой), праймера – 0,3 л/м².
- Объем песка для устройства основания приведен в спецификации с учетом коэффициента уплотнения 1,2.
- Класс бетонной поверхности принят А5 по ГОСТ 13015–2012.
- Крепление оборудования к фундаментам предусмотрено анкер-шпильками. Места крепления, количество и марку анкеров см. раздел ТР 24.150.04_2026.06.24 000 “Экомаш”.

						КПЭИ.1070/2.2-1.2-КЖ2			
						Комплекс по переработке «Новоселки»			
Изм.	Кол.уч.	Лист	№ док.	Подпись	Дата	Производственный корпус. Цех сортировки ТК0	Стадия	Лист	Листов
Разраб.	Висицкая			<i>В.И.</i>	04.26		Р	4	
Проверил	Висицкий			<i>В.И.</i>	04.26				
Н. контр.	Висицкий			<i>В.И.</i>	04.26	Фундамент ФМП2 (опалубка)	ООО «ТЭП ИВАНОВО»		
ГИП	Сильверстов			<i>С.И.</i>	04.26				

Согласовано		
	Взам. инв. №	
Инв. № подл.	Подп. и дата	

Фундамент ФМП2
(армирование)

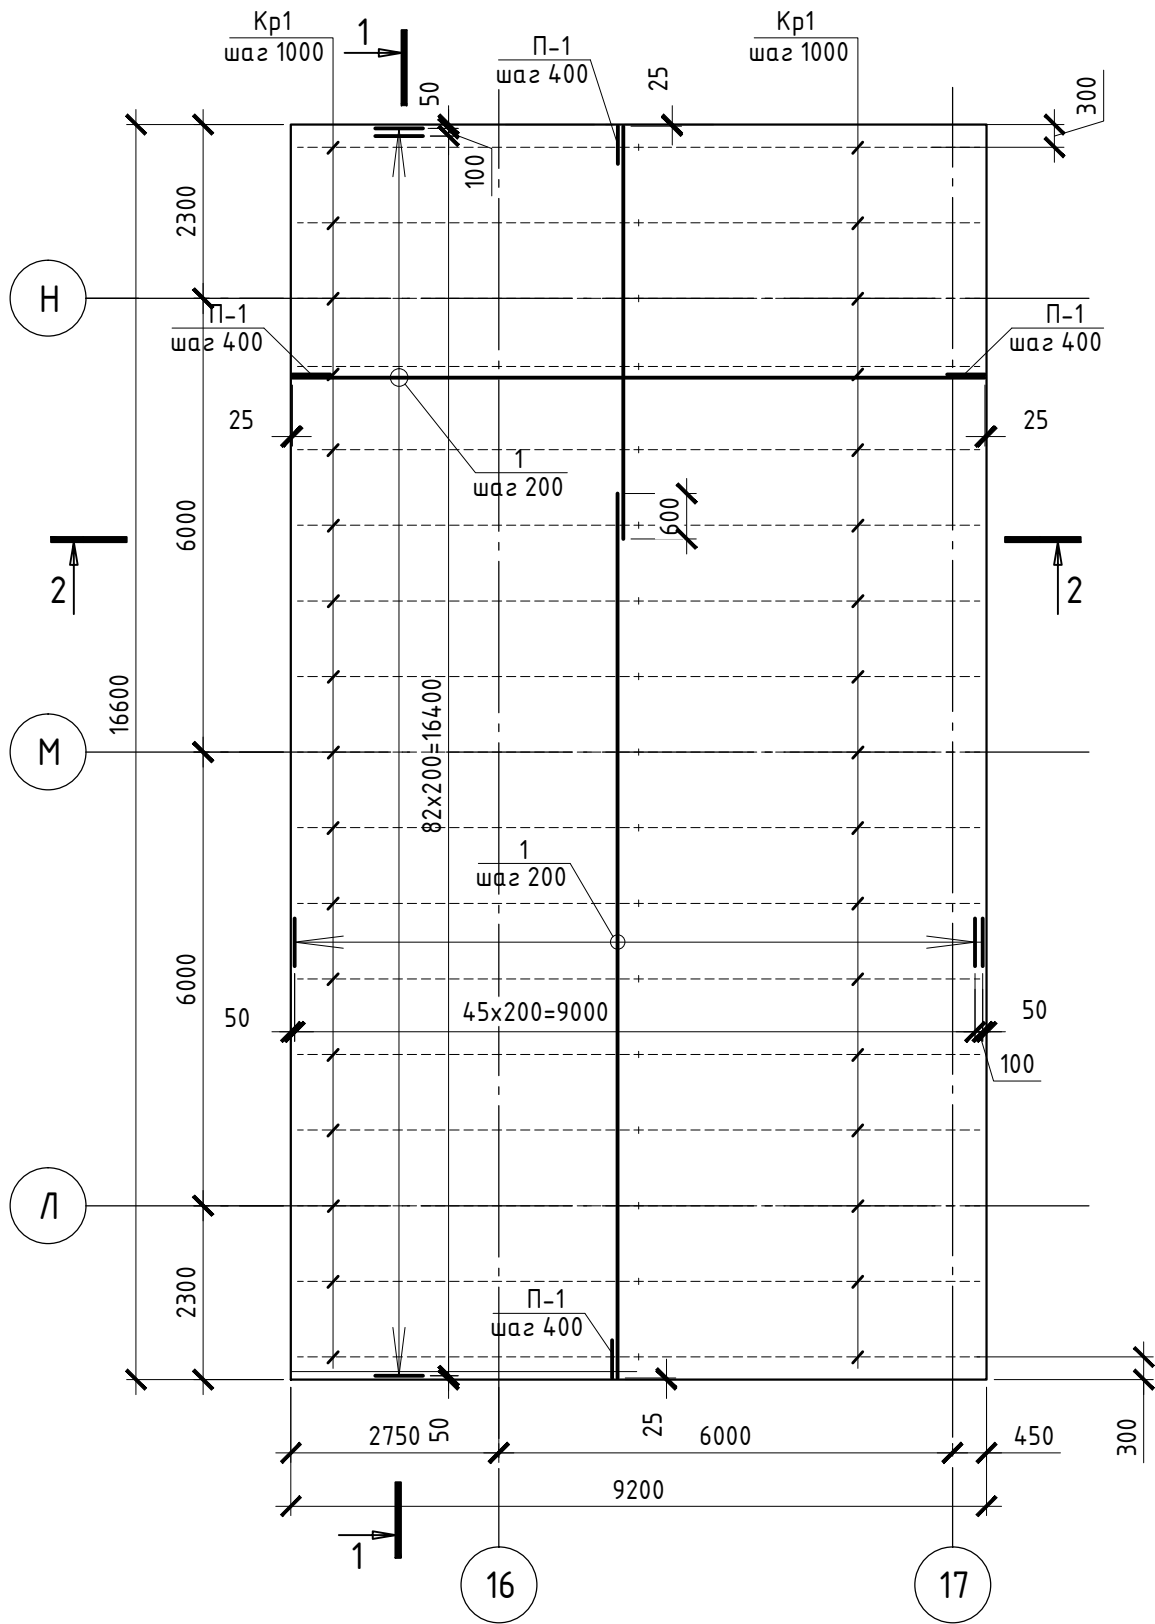


Ведомость деталей

Поз.	Эскиз
П-1	


Спецификация элементов монолитного фундамента ФМП2

Поз.	Обозначение	Наименование	Кол.	Масса ед. кг	Прим.
Кр1		Каркас Кр1	м.п.	311,1	2,3
1	ГОСТ 34028-2016	12-A500C	м.п.	3149,3	0,89 2802,88
2	ГОСТ 34028-2016	12-A500C	l=350	459	0,31
П-1	ГОСТ 34028-2016	12-A500C	l=1900	128	1,7
		Каркас Кр1		2,3	
3	ГОСТ 34028-2016	12-A500C	l=370	3	0,33
4	ГОСТ 34028-2016	10-A500C	l=1000	2	0,62


Узел стыка арматуры

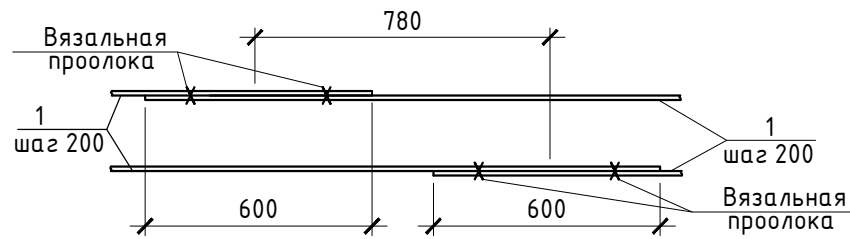


Каркас Кр1

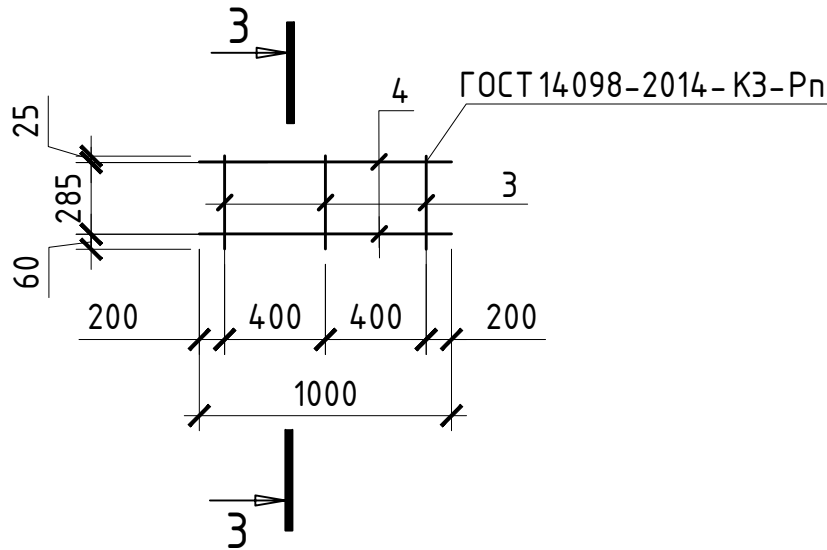


3-3

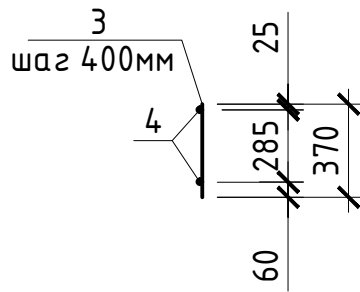

1-1(армирование)



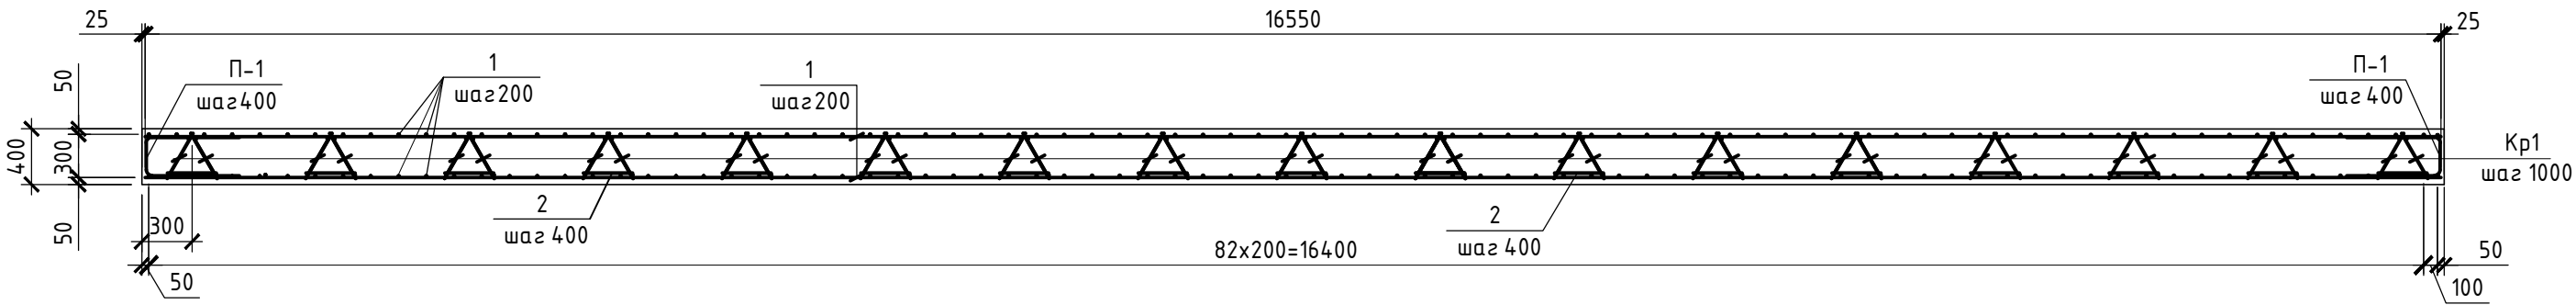


2-2(армирование)

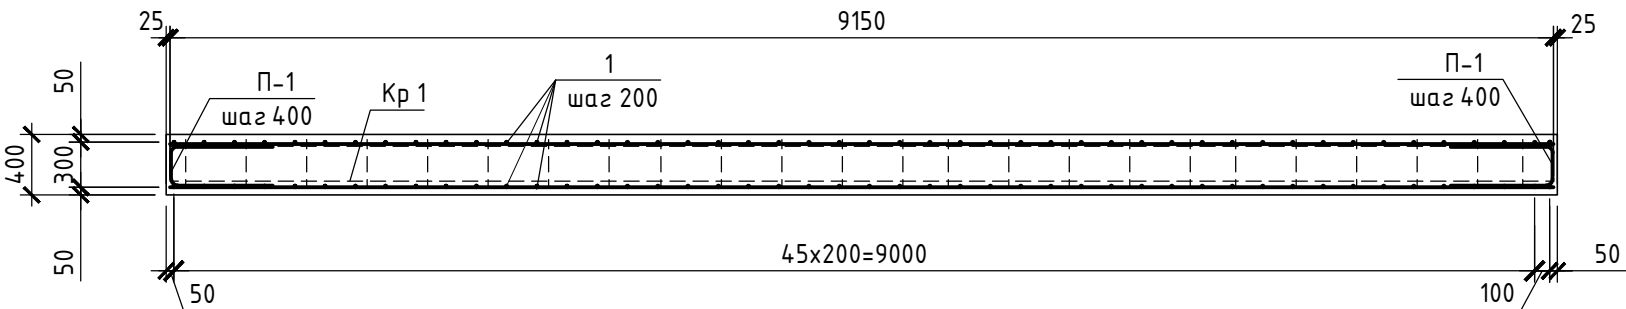

- Данный лист см. совместно с листом 2,4.
- Сварку каркасов производить в построечных условиях контактно-точечной электросваркой в соответствии с требованиями ГОСТ 15878-79.
- Для поддерживающих каркасов установить распорки (поз.2), связывающих каркасы в уровне нижних продольных стержней. Крепление стержней к каркасам выполняется при помощи вязальной проволоки (расход 12,6 кг).
- Объединение арматурных изделий и элементов фундамента в единую пространственную конструкцию выполнять вязкой отожженной стальной проволокой d=1.2 мм (ГОСТ 3282-74*). Расход 68,3 кг.
- Угол установки каркасов определить по месту.

						КПЭИ.1070/2.2-1.2-КЖ2			
						Комплекс по переработке «Новоселки»			
Изм.	Кол.уч.	Лист	№ док.	Подпись	Дата	Производственный корпус. Цех сортировки ТК0	Стадия	Лист	Листов
Разраб.	Висицкая			<i>В.В.</i>	04.26		Р	5	
Проверил	Висицкий			<i>В.В.</i>	04.26	Фундамент ФМП2 (армирование)	ООО «ТЭП ИВАНОВО»		
Н. контр.	Висицкий			<i>В.В.</i>	04.26				
ГИП	Сильверстов			<i>В.В.</i>	04.26				

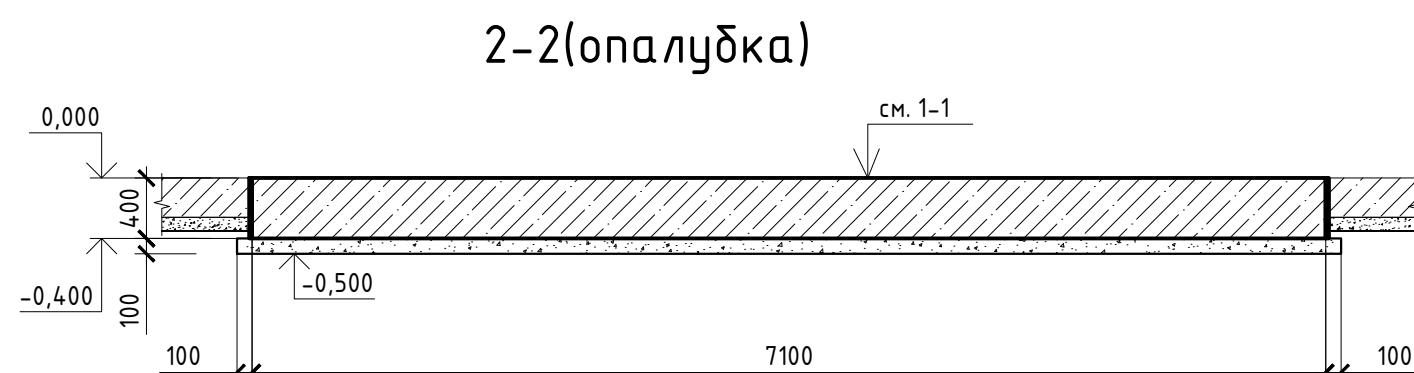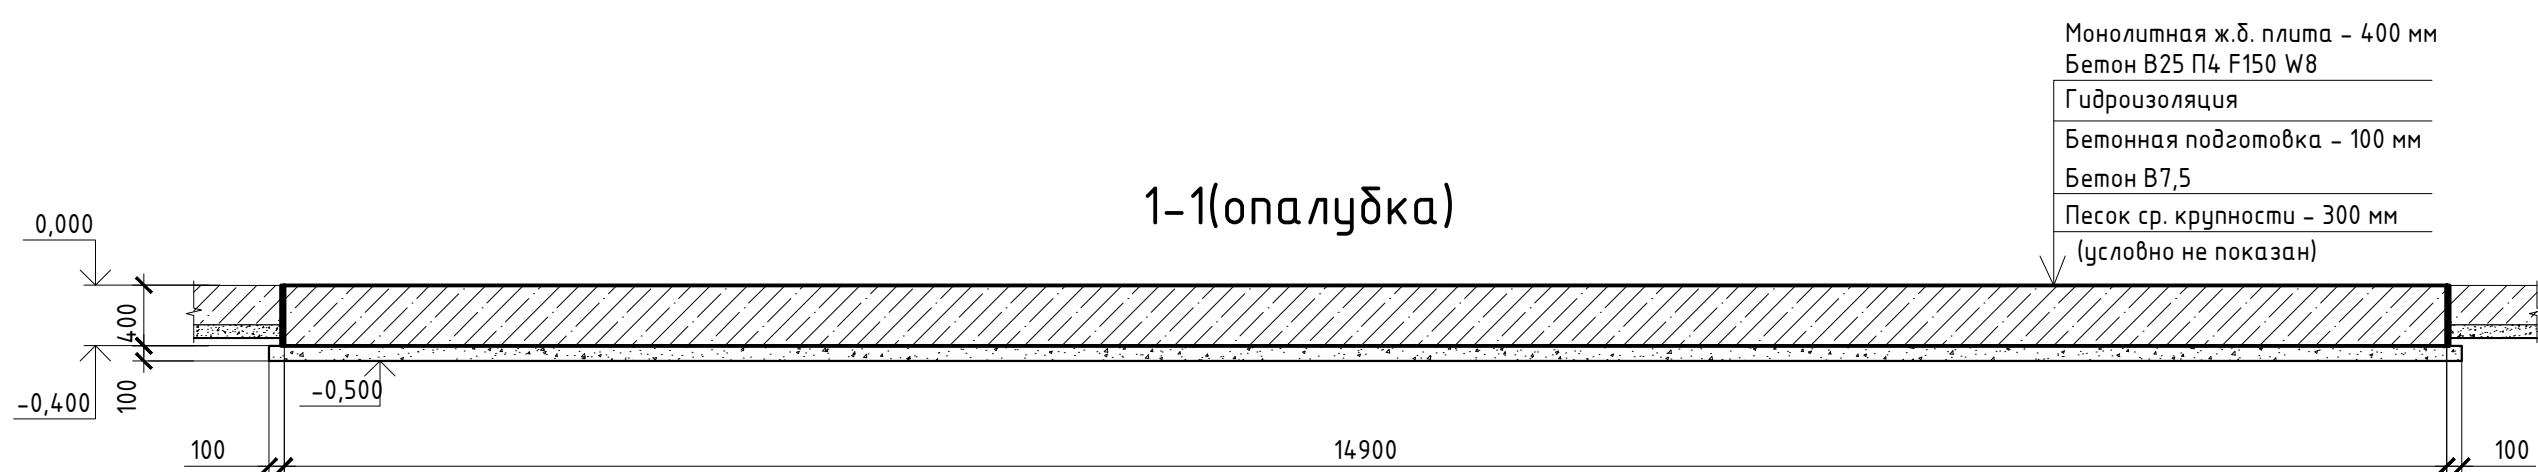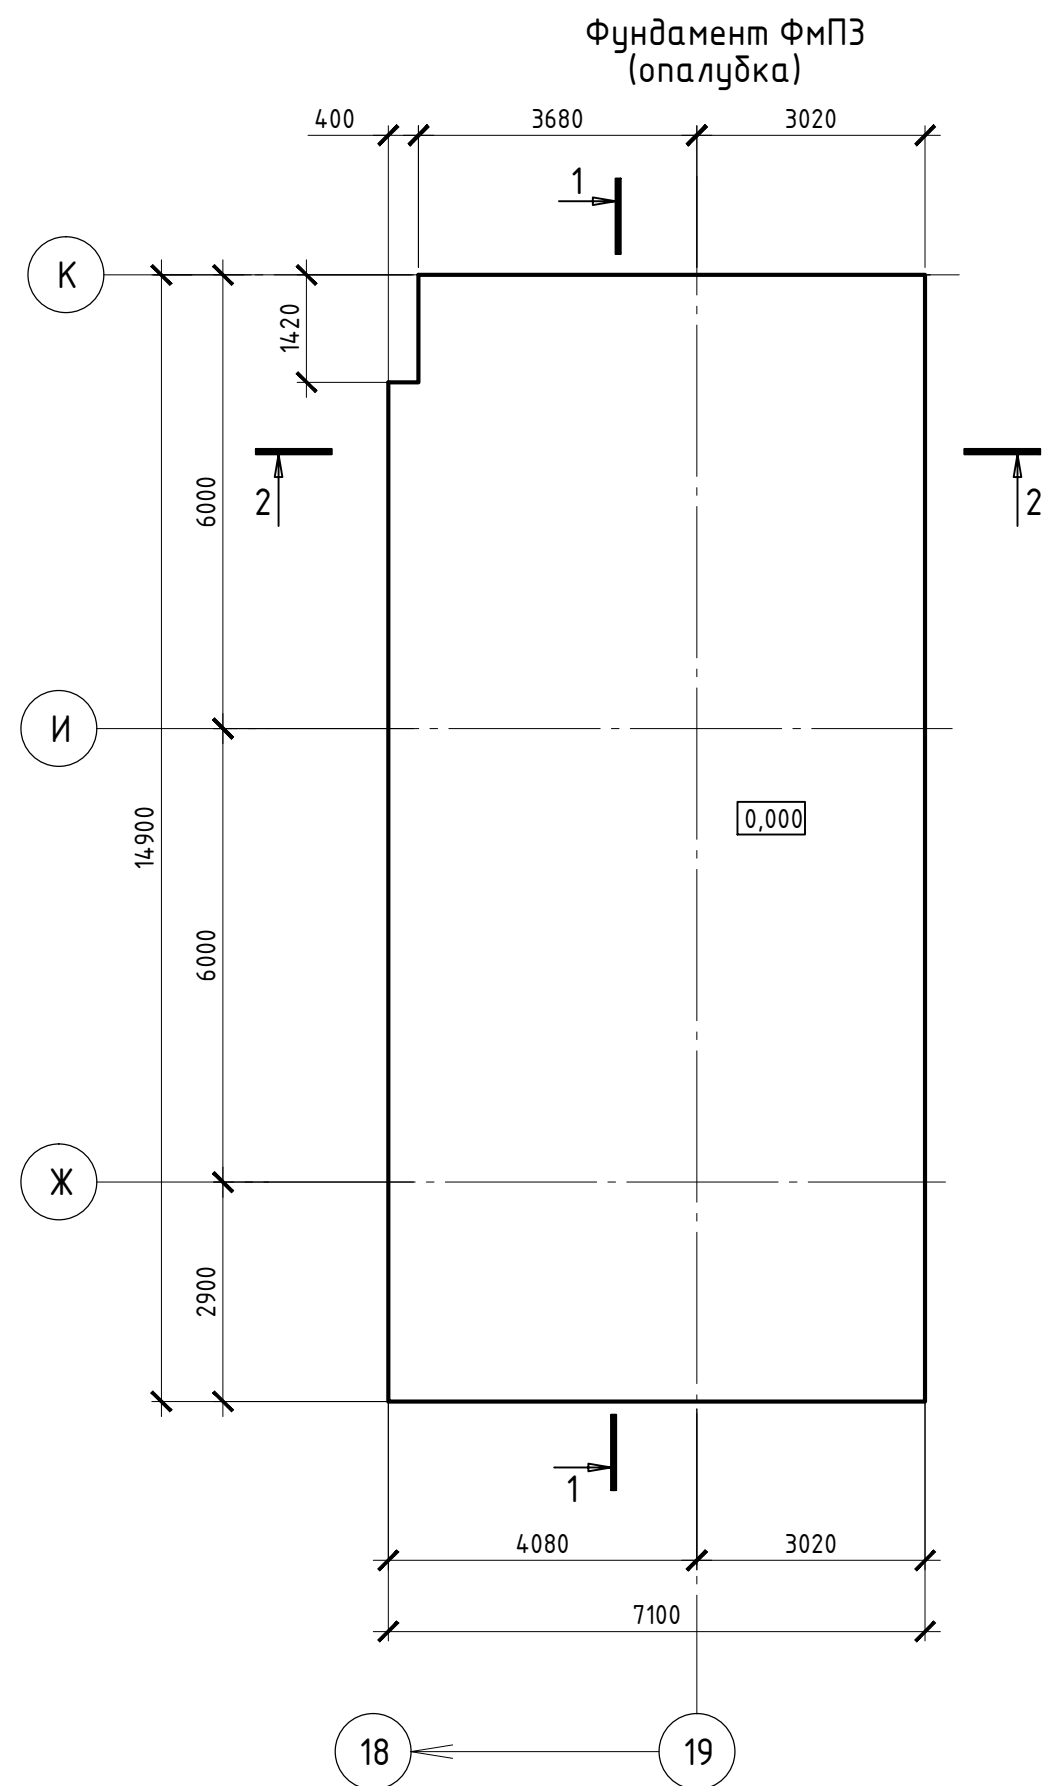


Поз.	Обозначение	Наименование	Кол.	Масса ед. кг	Прим.
		Материалы:			
	ГОСТ 26633-2015	Бетон В25 П4 F150 W8	м ³	42,4	
	ГОСТ 26633-2015	Бетон В7,5	м ³	11,1	
	ГОСТ 8736-2025	Песок ср.крупности	м ³	41,4	
	ТУ 5775-011-17925162-2003	Праймер битумный ТЕХНОНИКОЛЬ №01	124,1 м ²	37,3	0,3 л/м ²
	ТУ 5775-034-17925162-2005	Битумная мастика ТЕХНОНИКОЛЬ №24 (2 слоя)	124,1 м ²	248,2	2,0 кг/м ² (на 2 слоя)

1. Общие указания см. на листе 1.
2. Данный лист см. совместно с листами 2, 5.
3. Боковые поверхности фундамента и горизонтальную поверхность бетонной подготовки обработать гидроизоляционной мастикой Технониколь №24 (2 слоя) по слою битумного праймера.
Расход мастики – 1,0 кг/м² (на 1 слой), праймера – 0,3 л/м².
4. Объем песка для устройства основания приведен в спецификации с учетом коэффициента уплотнения 1,2.
5. Класс бетонной поверхности принят А5 по ГОСТ 13015–2012.
6. Крепление оборудования к фундаментам предусмотрено анкер-шпильками. Места крепления, количество и марку анкеров см. раздел TP 24.150.04 2026.07.21–КХ 000 "Экомаш".

						КПЭИ.1070/2.2-1.2-КЖ2				
1	-	Зам.	4219-26	<i>РЗ</i>	27.07.26	Комплекс по переработке «Новоселки»				
Изм.	Кол.уч.	Лист	№ док.	Подпись	Дата	Производственный корпус. Цех сортировки ТК0		Стадия	Лист	Листов
Разраб.		Висущая		<i>РЗ</i>	04.26			Р	6	
Проверил		Висущий		<i>С.В.</i>	04.26	Фундамент ФМПЗ (опалубка)		ООО «ТЭП ИВАНОВО»		
Н. контр.		Висущий		<i>С.В.</i>	04.26					
ГИП		Сильверстов		<i>Сильверстов</i>	04.26					

Согласовано		
Взам. инв. №		
Подп. и дата		
Инв. № подл.		


Фундамент ФМПЗ
(армирование)

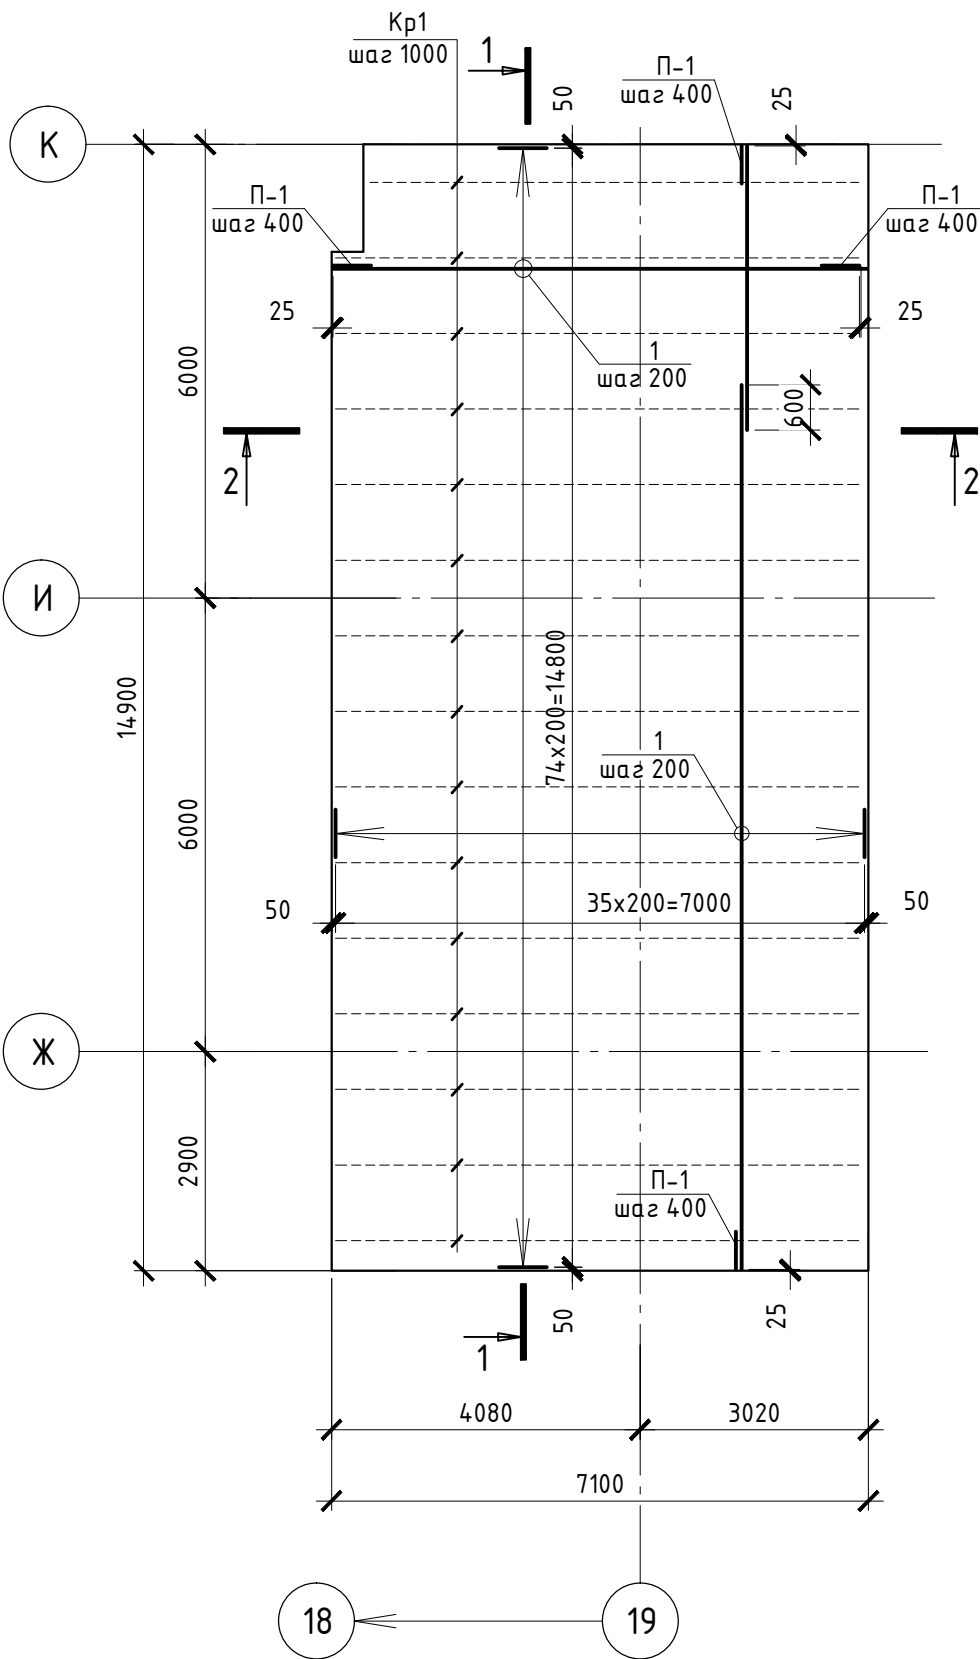


Ведомость деталей

Поз.	Эскиз
П-1	


Узел стыка арматуры

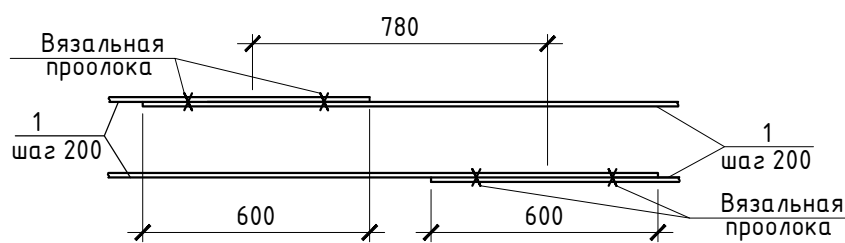


Каркас Кр1

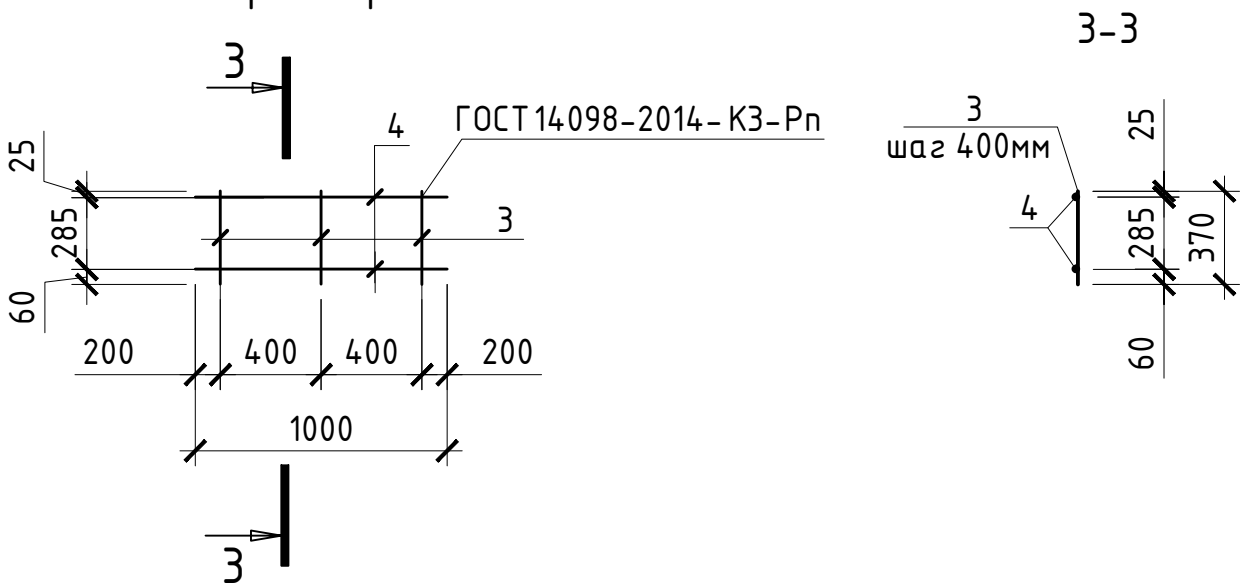

1-1 (армирование)

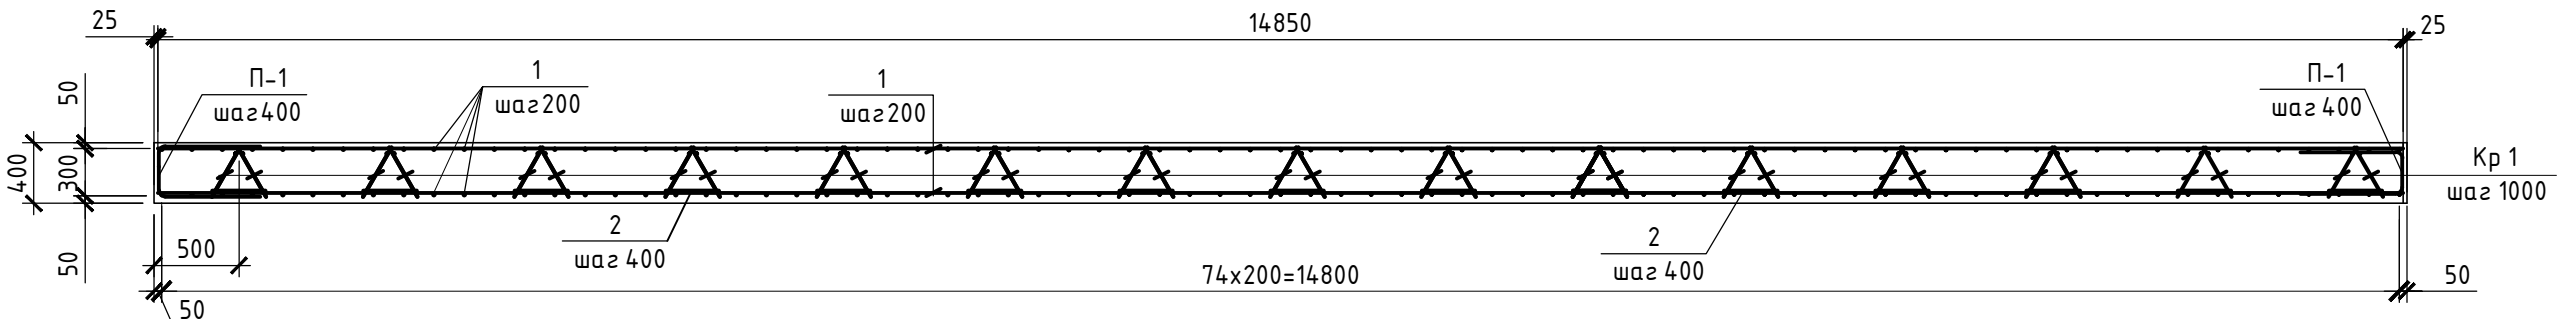

2-2 (армирование)

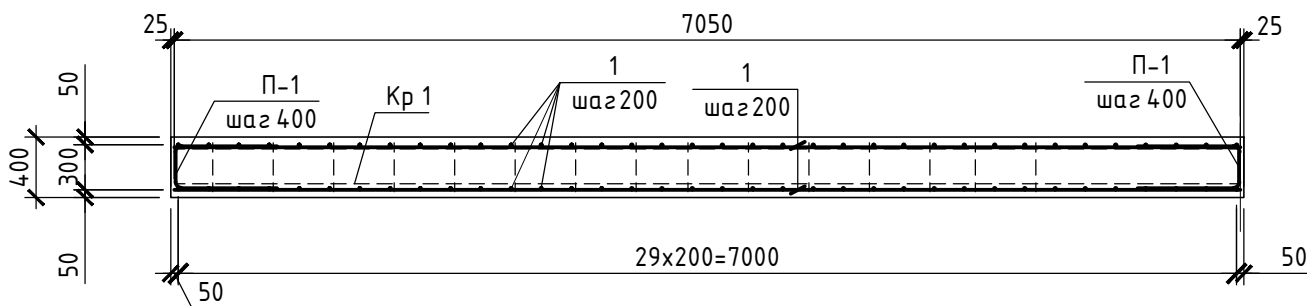

Спецификация элементов монолитного фундамента ФМПЗ


Поз.	Обозначение	Наименование	Кол.	Масса ед. кг	Прим.
Кр1		Каркас Кр1	м.п.	225,6	2,3
1	ГОСТ 34028-2016	12-A500C	м.п.	2148,3	0,89 1912,0
2	ГОСТ 34028-2016	12-A500C	l=350	135	0,31
П-1	ГОСТ 34028-2016	12-A500C	l=1900	111	1,7
		Каркас Кр1		2,3	
3	ГОСТ 34028-2016	12-A500C	l=370	3	0,33
4	ГОСТ 34028-2016	10-A500C	l=1000	2	0,62

Ведомость расхода стали

Марка элемента	Изделия арматурные				Общий расход
	Арматура класса			Всего	
	А500С				
	ГОСТ 34028-2016				
	φ10	φ12	Итого		
ФМПЗ	279,8	2365,9	2645,7	2645,7	2645,7

- Данный лист см. совместно с листом 2,7.
- Сварку каркасов производить в построчных условиях контактно-точечной электросваркой в соответствии с требованиями ГОСТ 15878-79.
- Для поддерживающих каркасов установить распорки (поз.2), связывающих каркасы в уровне нижних продольных стержней. Крепление стержней к каркасам выполняется при помощи вязальной проволоки (расход 10,5 кг).
- Объединение арматурных изделий и элементов фундамента в единую пространственную конструкцию выполнять вязкой отожженной стальной проволокой d=1.2 мм (ГОСТ 3282-74*). Расход 36,8 кг.
- Угол установки каркасов определить по месту.

							КПЭИ.1070/2.2-1.2-КЖ2			
							Комплекс по переработке «Новоселки»			
1	-	Зам.	4.219-26	РБ	27.07.26		Производственный корпус. Цех сортировки ТК0	Стадия	Лист	Листов
Изм.	Кол.уч.	Лист	№ док.	Подпись	Дата			Р	7	
Разраб.	Висицкая			РБ	04.26					
Проверил	Висицкий			СВ	04.26		Фундамент ФМПЗ (армирование)	ООО «ТЭП ИВАНОВО»		
Н. контр.	Висицкий			СВ	04.26					
ГИП	Сильверстов			СВ	04.26					

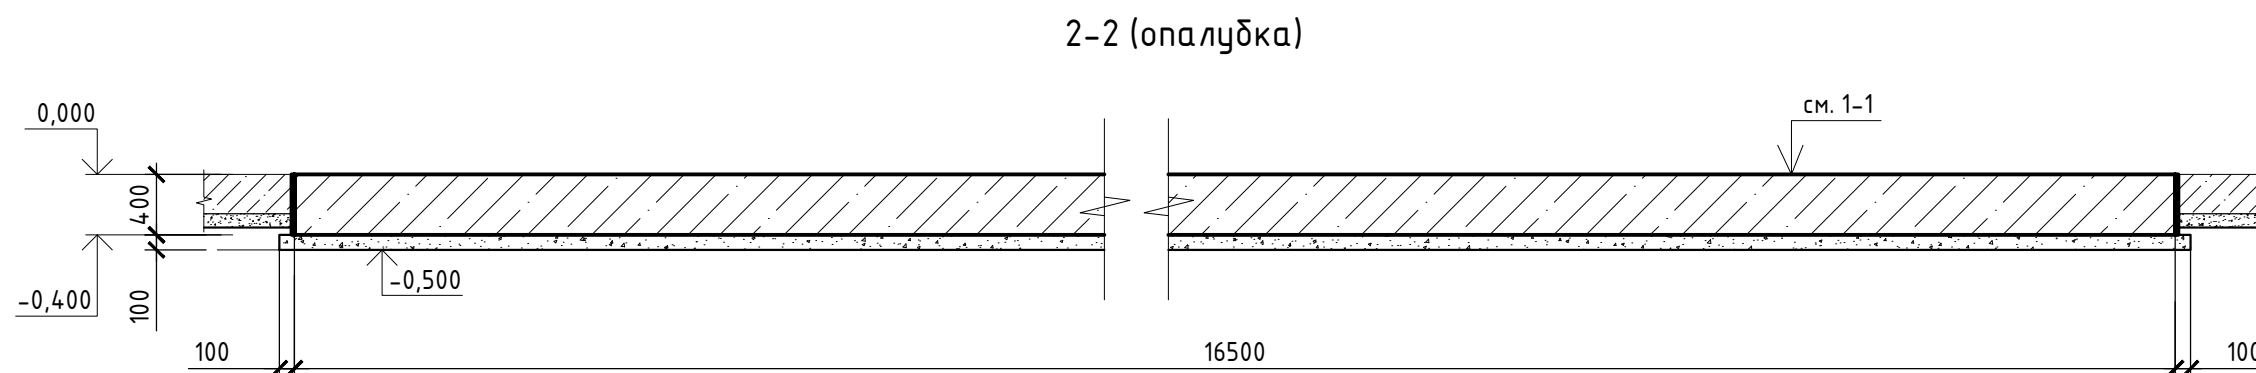

1. Общие указания см. на листе 1.
2. Данный лист см. совместно с листами 2, 5.
3. Боковые поверхности фундамента и горизонтальную поверхность бетонной подготовки обработать гидроизоляционной мастикой Технониколь №24 (2 слоя) по слою битумного праймера.
Расход мастики—1,0 кг/м² (на 1 слой), праймера — 0,3 л/м².
4. Объем песка для устройства основания приведен в спецификации с учетом коэффициента уплотнения 1,2.
5. Класс бетонной поверхности принят А5 по ГОСТ 13015–2012.
6. Крепление оборудования к фундаментам предусмотрено анкер-шпильками. Места крепления, количество и марку анкероб см. раздел TP 24.150.04_2026.06.24 000 "Экомаш".

Формат А2

Architectural floor plan of a rectangular building with a grid system. The plan shows a central hall (88x200=17600) and a corridor (68x200=13600). The building is divided into three horizontal sections (Б, В, Г) and three vertical sections (9, 10, 11). Dimensions are given in millimeters. The plan includes various structural details, such as walls, doors, and windows, and is labeled with 'Kp1' and 'П-1'.

Поз.	Эскиз
П-1	

Поз.	Обозначение	Наименование	Кол.	Масса ед. кг	Прим.	
Кр1		Каркас Кр1	м.п.	495,0	2,3	
1	ГОСТ 34028-2016	12-А500С	м.п.	5187,5	0,89	4616,9
2	ГОСТ 34028-2016	12-А500С	l=350	738	0,31	
П-1	ГОСТ 34028-2016	12-А500С	l=1900	160	1,7	
		Каркас Кр1			2,3	
3	ГОСТ 34028-2016	12-А500С	l=370	3	0,33	
4	ГОСТ 34028-2016	10-А500С	l=1000	2	0,62	

Марка элемента	Изделия арматурные				Общий расход			
	Арматура класса			Всего				
	А500С							
	ГОСТ 34028-2016							
	Ø10	Ø12	Итого					
ФМП4	613,8	5607,73	6221,53	6221,53	6221,53			

Technical drawing of a bridge structure, showing a side elevation and a plan view.

Side Elevation:


- Total length: 17750
- Height: 25
- Labels: $\Pi-1$ (width ≥ 400), 1 (width ≥ 200), 2 (width ≥ 400), $Kp1$ (width ≥ 1000).
- Dimensions: 400, 300, 50, 375, 50.

Plan View:


- Total width: 17600 (88x200)
- Height: 25
- Labels: $\Pi-1$ (width ≥ 400), 1 (width ≥ 200), 2 (width ≥ 400), $Kp1$ (width ≥ 1000).
- Dimensions: 100, 50.

Technical drawing of a reinforced concrete slab (Kp 1) with dimensions and reinforcement details. The drawing shows a cross-section of the slab with a width of 400 mm and a height of 300 mm. The reinforcement consists of top bars (labeled П-1, $\text{шаг } 400$) and bottom bars (labeled 1, $\text{шаг } 200$). The slab is supported by walls on both sides. The overall length of the slab is 13750 mm. The distance between the centerlines of the supports is 68x200=13600 mm. The drawing also shows the thickness of the slab at the supports (50 mm) and the distance from the centerline to the edge of the support (100 mm).

- | | | | | | | | | | | |
|-----------|-------------|------|--------|-------------------------|-------|--|--|-------------------|------|--------|
| | | | | | | КПЭИ.1070/2.2-1.2-КЖ2 | | | | |
| | | | | | | Комплекс по переработке «Новоселки» | | | | |
| Изм. | Кол.уч. | Лист | № док. | Подпись | Дата | Производственный корпус.
Цех сортировки ТК0 | | Стадия | Лист | Листов |
| Разраб. | Висицкая | | | <i>В.В. Висицкая</i> | 04.26 | | | Р | 9 | |
| Проверил | Висицкий | | | <i>В.В. Висицкий</i> | 04.26 | Фундамент ФМП4
(армирование) | | ООО «ТЭП ИВАНОВО» | | |
| Н. контр. | Висицкий | | | <i>В.В. Висицкий</i> | 04.26 | | | | | |
| ГИП | Сильверстов | | | <i>В.В. Сильверстов</i> | 04.26 | | | | | |

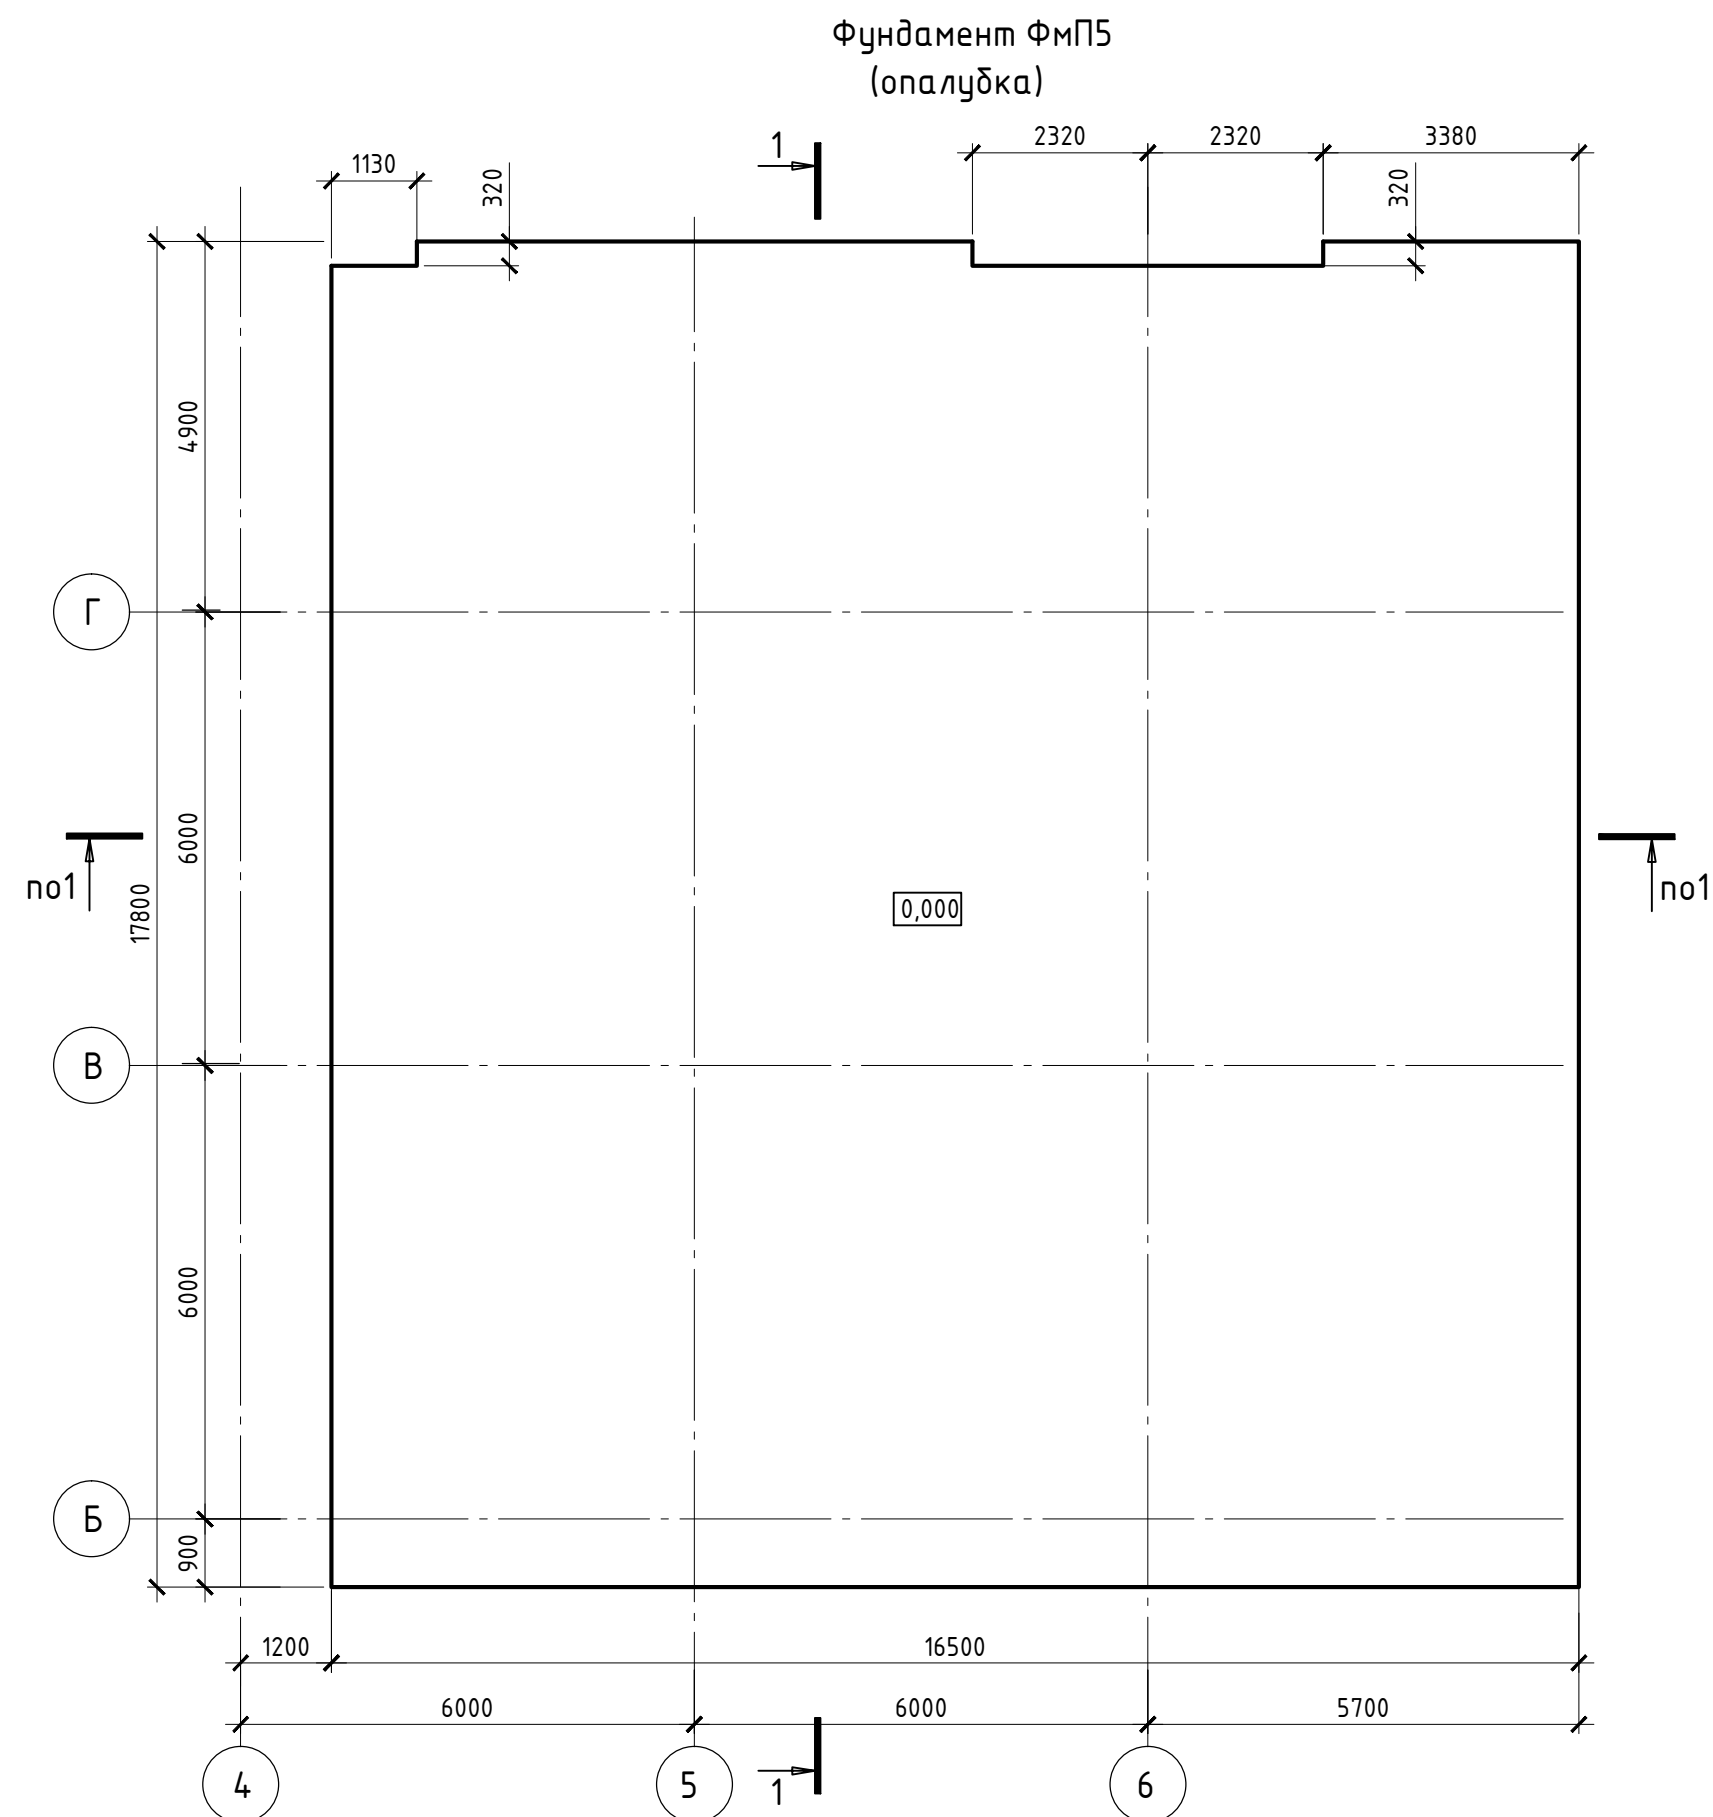

Фундамент ФМП5
(армирование)

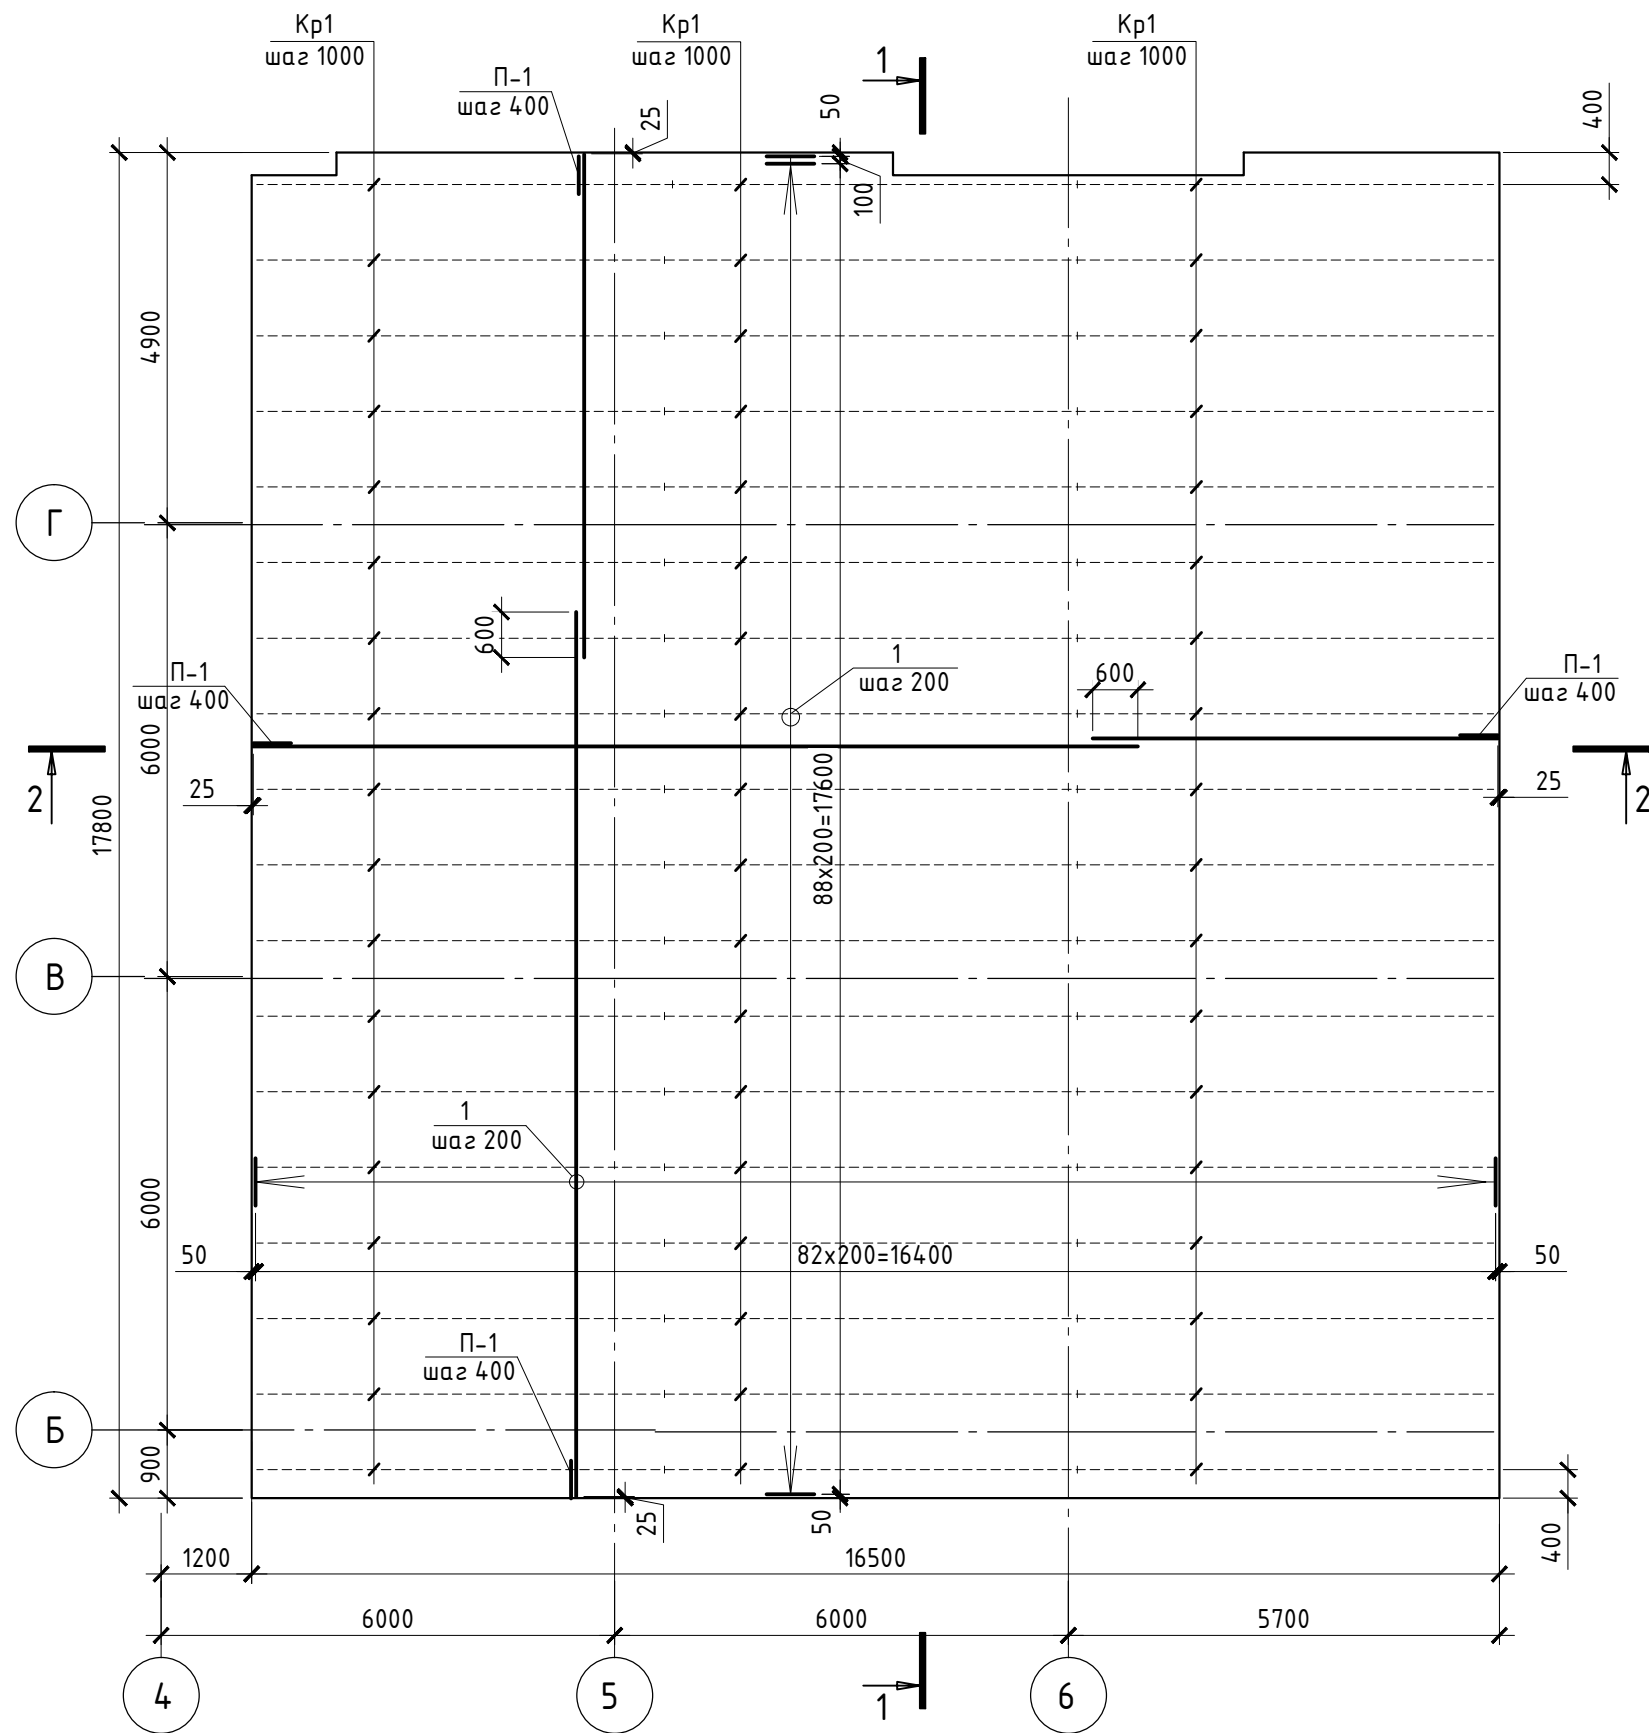


Ведомость деталей

Поз.	Эскиз
П-1	

Спецификация элементов монолитного фундамента ФМП5

Поз.	Обозначение	Наименование	Кол.	Масса ед. кг	Прим.
Кр1		Каркас Кр1	м.п.	592,2	2,3
1	ГОСТ 34028-2016	12-A500C	м.п.	6115,1	0,89 5442,44
2	ГОСТ 34028-2016	12-A500C	l=350	738	0,31
П-1	ГОСТ 34028-2016	12-A500C	l=1900	172	1,7
		Каркас Кр1		2,3	
3	ГОСТ 34028-2016	12-A500C	l=370	3	0,33
4	ГОСТ 34028-2016	10-A500C	l=1000	2	0,62


Узел стыка арматуры

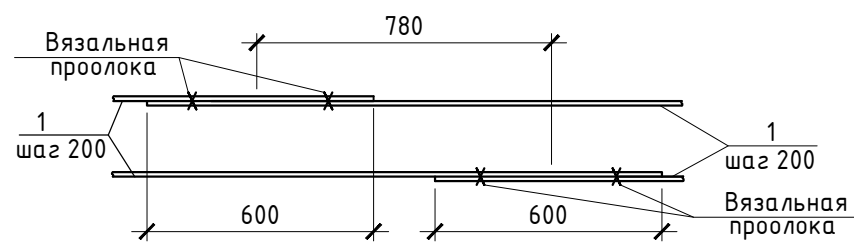


Ведомость расхода стали

Марка элемента	Изделия арматурные				Общий расход
	Арматура класса			Всего	
	А500С				
	ГОСТ 34028-2016				
	Ø10	Ø12	Итого		
ФМП5	367,2	6549,9	6917,1	6917,1	6917,1


Каркас Кр1

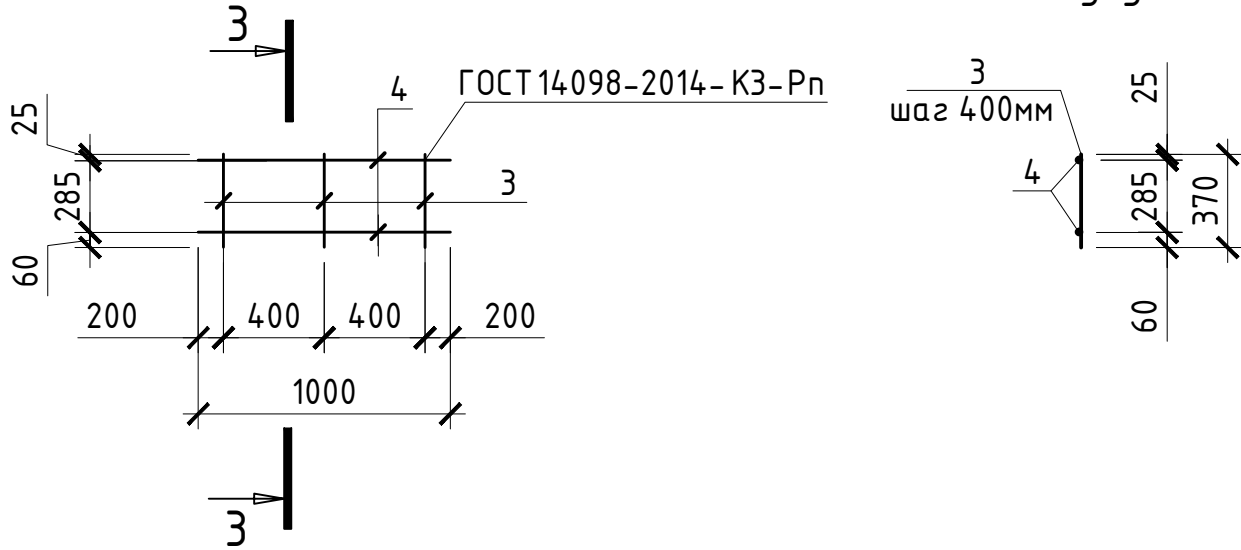

1-1 (армирование)

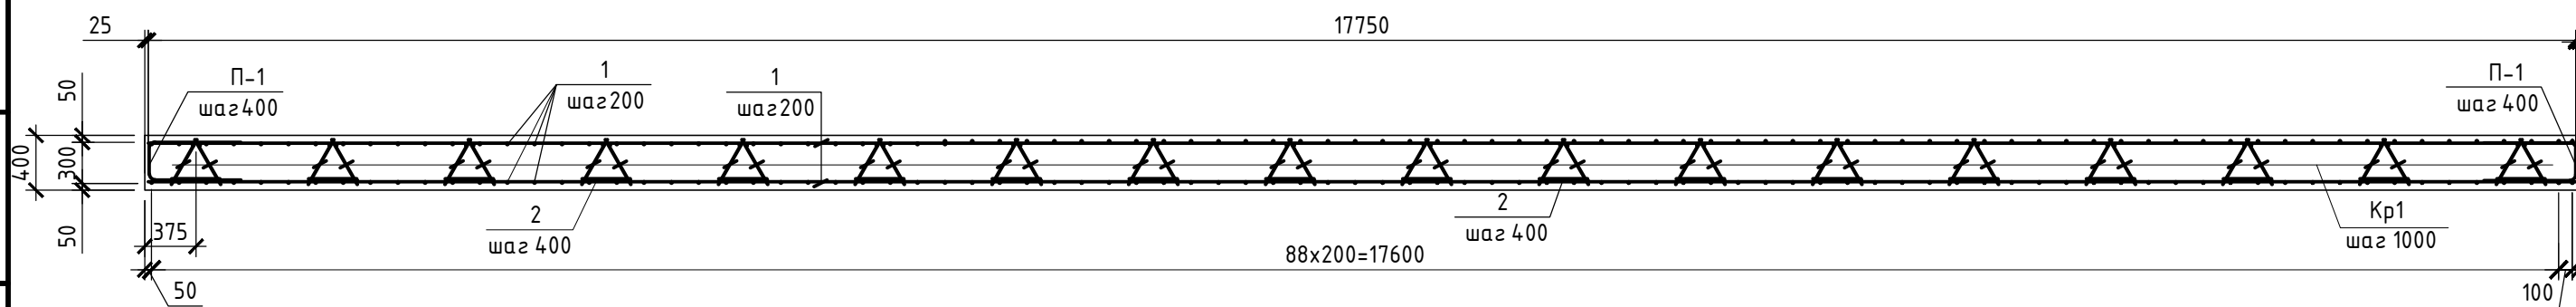

2-2 (армирование)

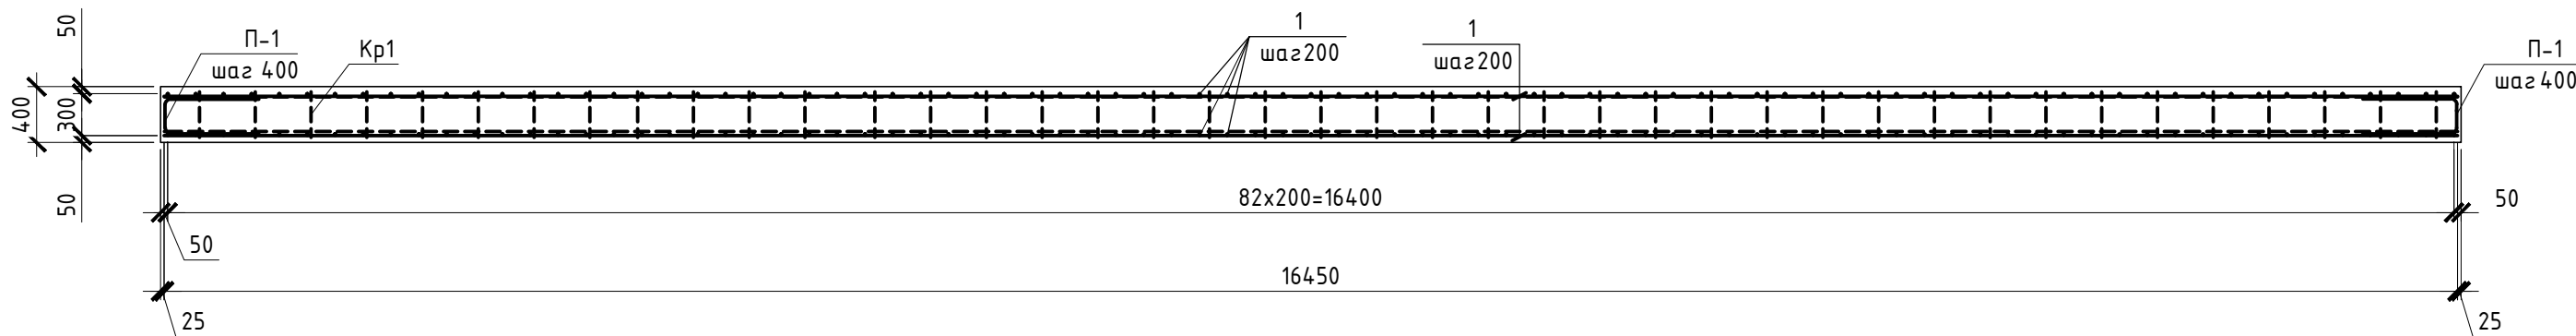

- Данный лист см. совместно с листом 2,10.
- Сварку каркасов производить в построечных условиях контактно-точечной электросваркой в соответствии с требованиями ГОСТ 15878-79.
- Для поддерживающих каркасов установить распорки (поз.2), связывающих каркасы в уровне нижних продольных стержней. Крепление стержней к каркасам выполняется при помощи вязальной проволоки (расход 24,2 кг).
- Объединение арматурных изделий и элементов фундамента в единую пространственную конструкцию выполнять вязкой отожженной стальной проволокой d=1.2 мм (ГОСТ 3282-74*). Расход 122,5 кг.
- Угол установки каркасов определить по месту.

КПЭИ.1070/2.2-1.2-КЖ2					
Комплекс по переработке «Новоселки»					
Изм.	Кол.уч.	Лист	№ док.	Подпись	Дата
Разраб.	Висицкая	Висицкий	Р	04.26	
Проверил	Висицкий	Висицкий	С	04.26	
Н. контр.	Висицкий	Висицкий	С	04.26	
ГИП	Сильверстов	Сильверстов	С	04.26	
Производственный корпус. Цех сортировки ТК0				Стадия	Лист
Фундамент ФМП5 (армирование)				Р	11
ООО «ТЭП ИВАНОВО»				Листов	